



Обмерный план участка

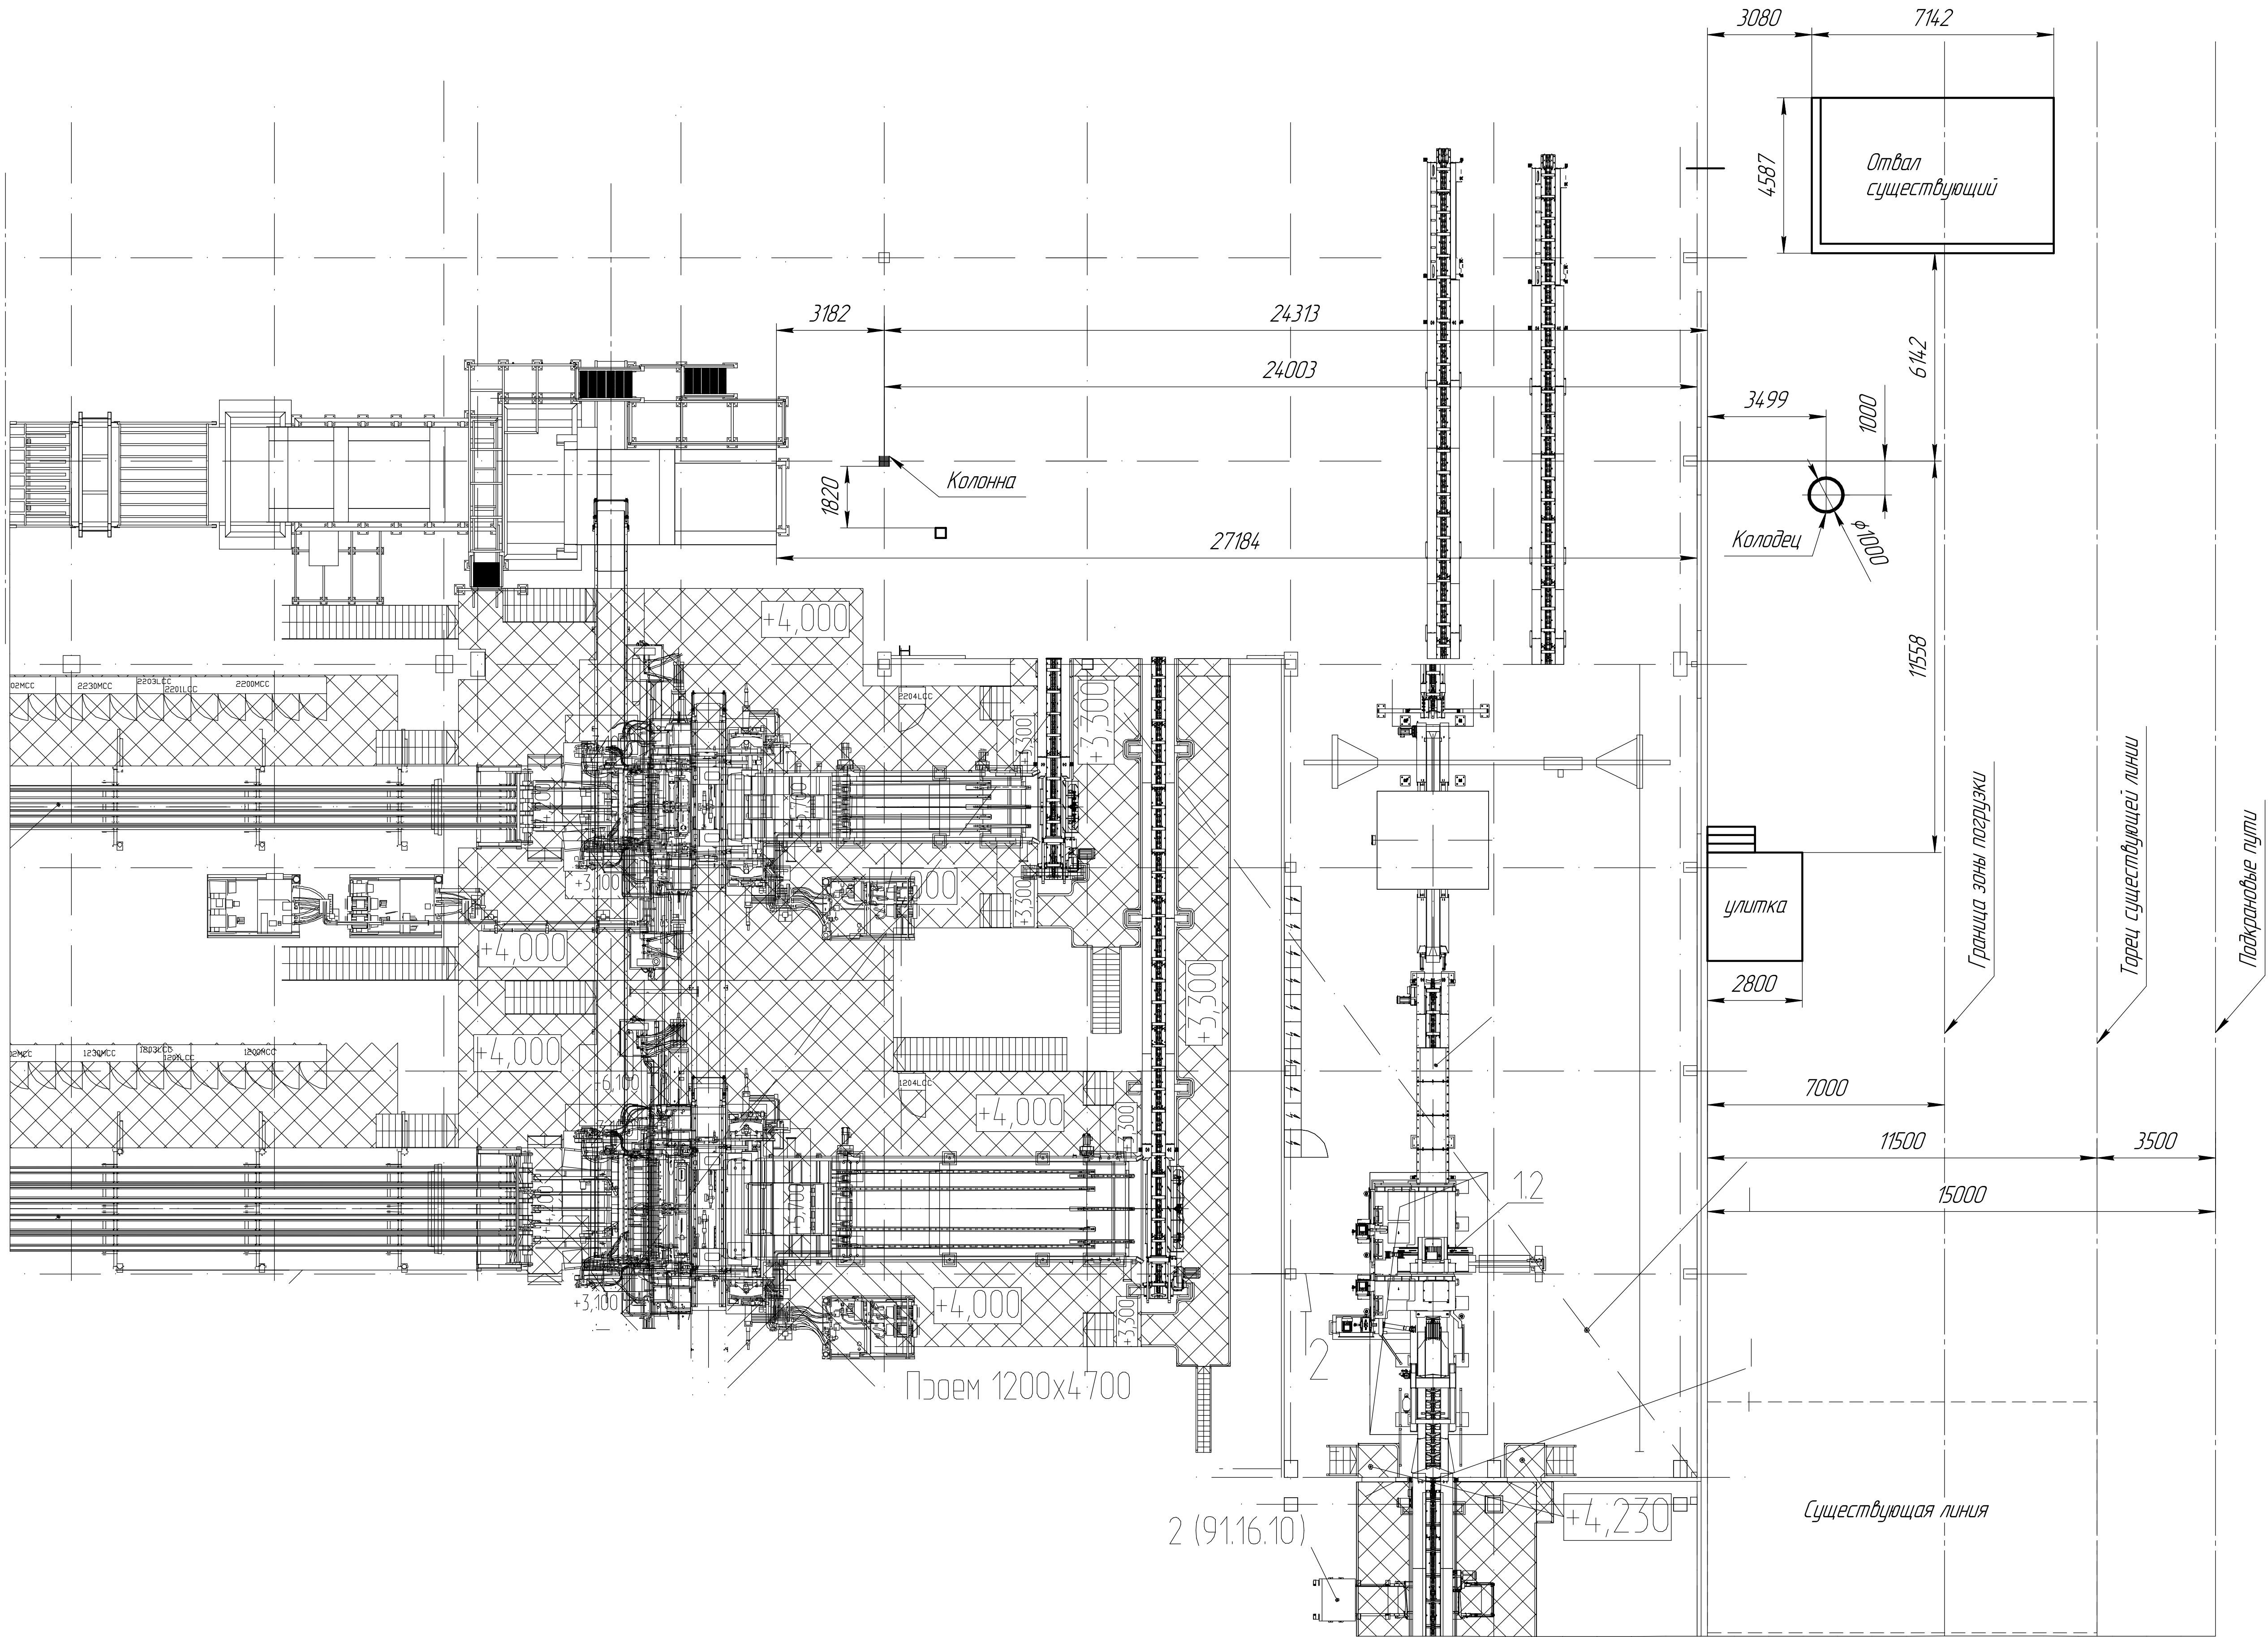

				Линия раскряжежки и подкрановых путей на линию дощевания		
				ООО «Галицкий фанерный комбинат»		
				План линии		
Изм.	Лист	№ док.	Подп.	Дат.	Лист	Масштаб
Разраб.					1122825,72	1:60
Проб.					Лист 1	Листов 6
Т.контр.					ООО "ПО "ДИАКОМ"	
Н.контр.					Формат А1	
Утв.					Копирован	

Схема расположения оборудования ПО "ДИАКОМ"

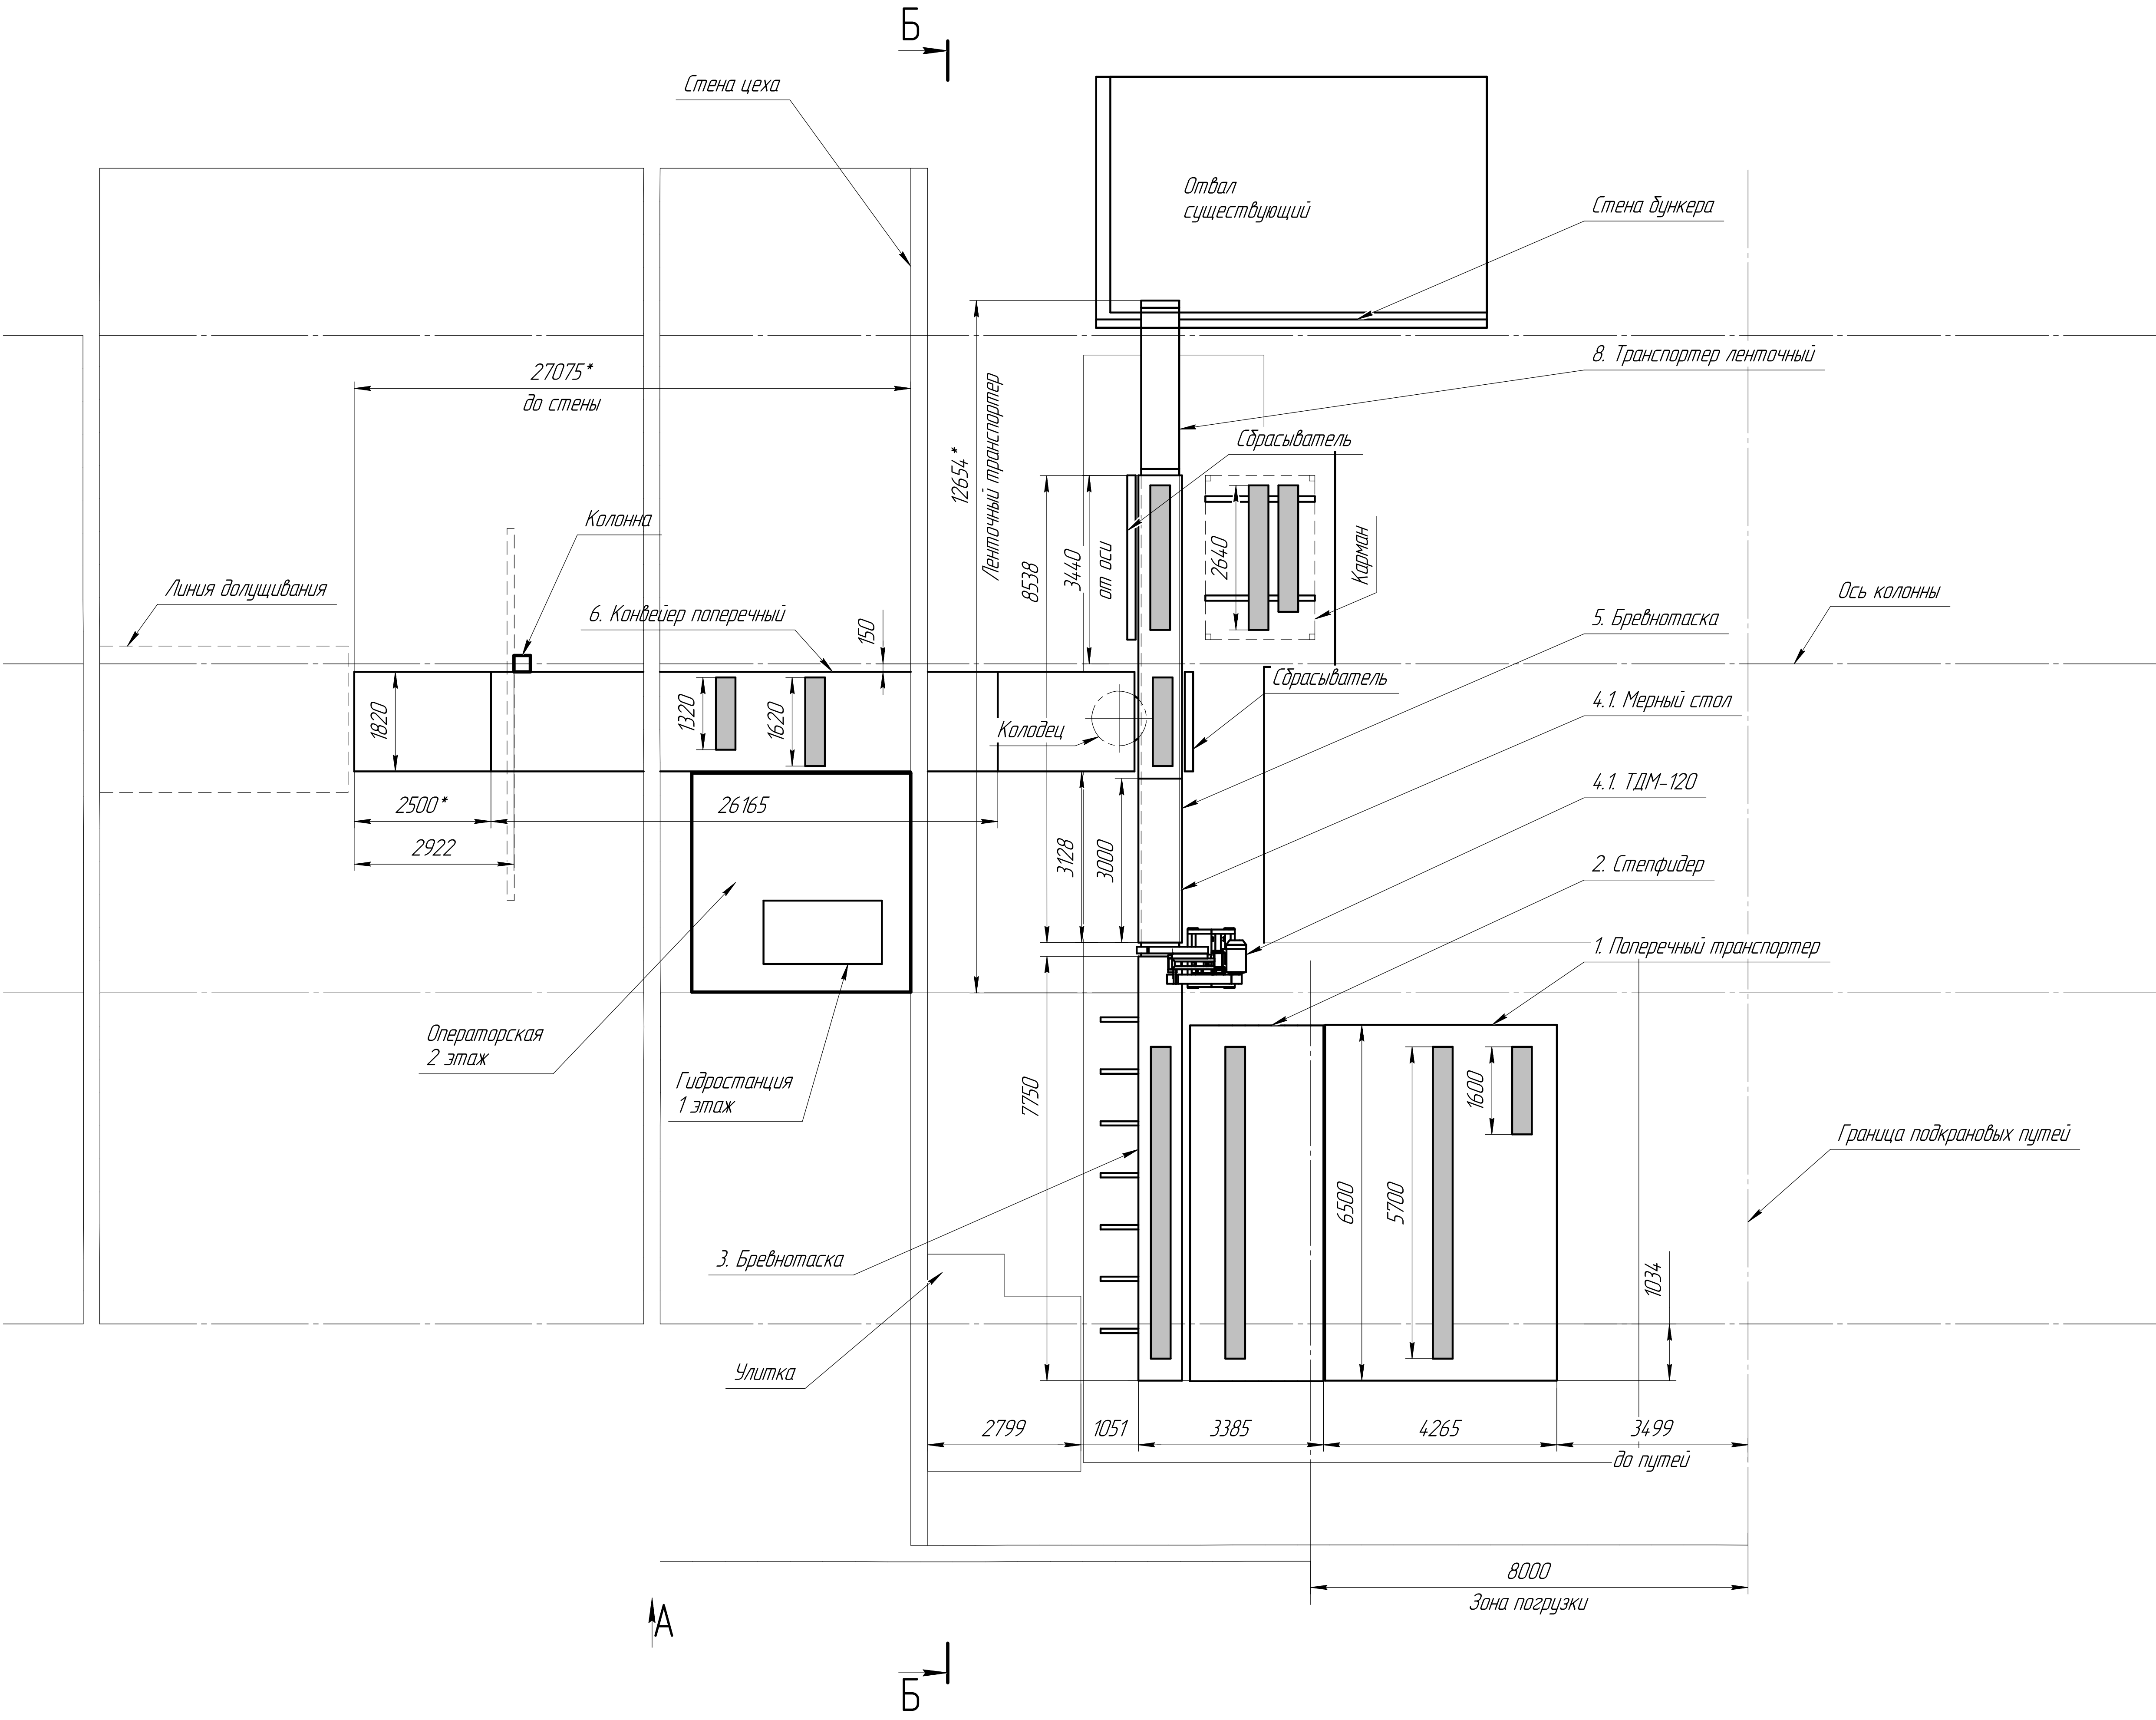

Изм.	Лист	№ докум.	Подп.	Дата

Лист	3
------	---


Формат А3



Копировал _____ Формат А3

План бетонной подготовки
под фундаментную плиту

Линия раскряжевки и подачи чураков на линию долуцивания
ООО «Галицкий фанерный комбинат»

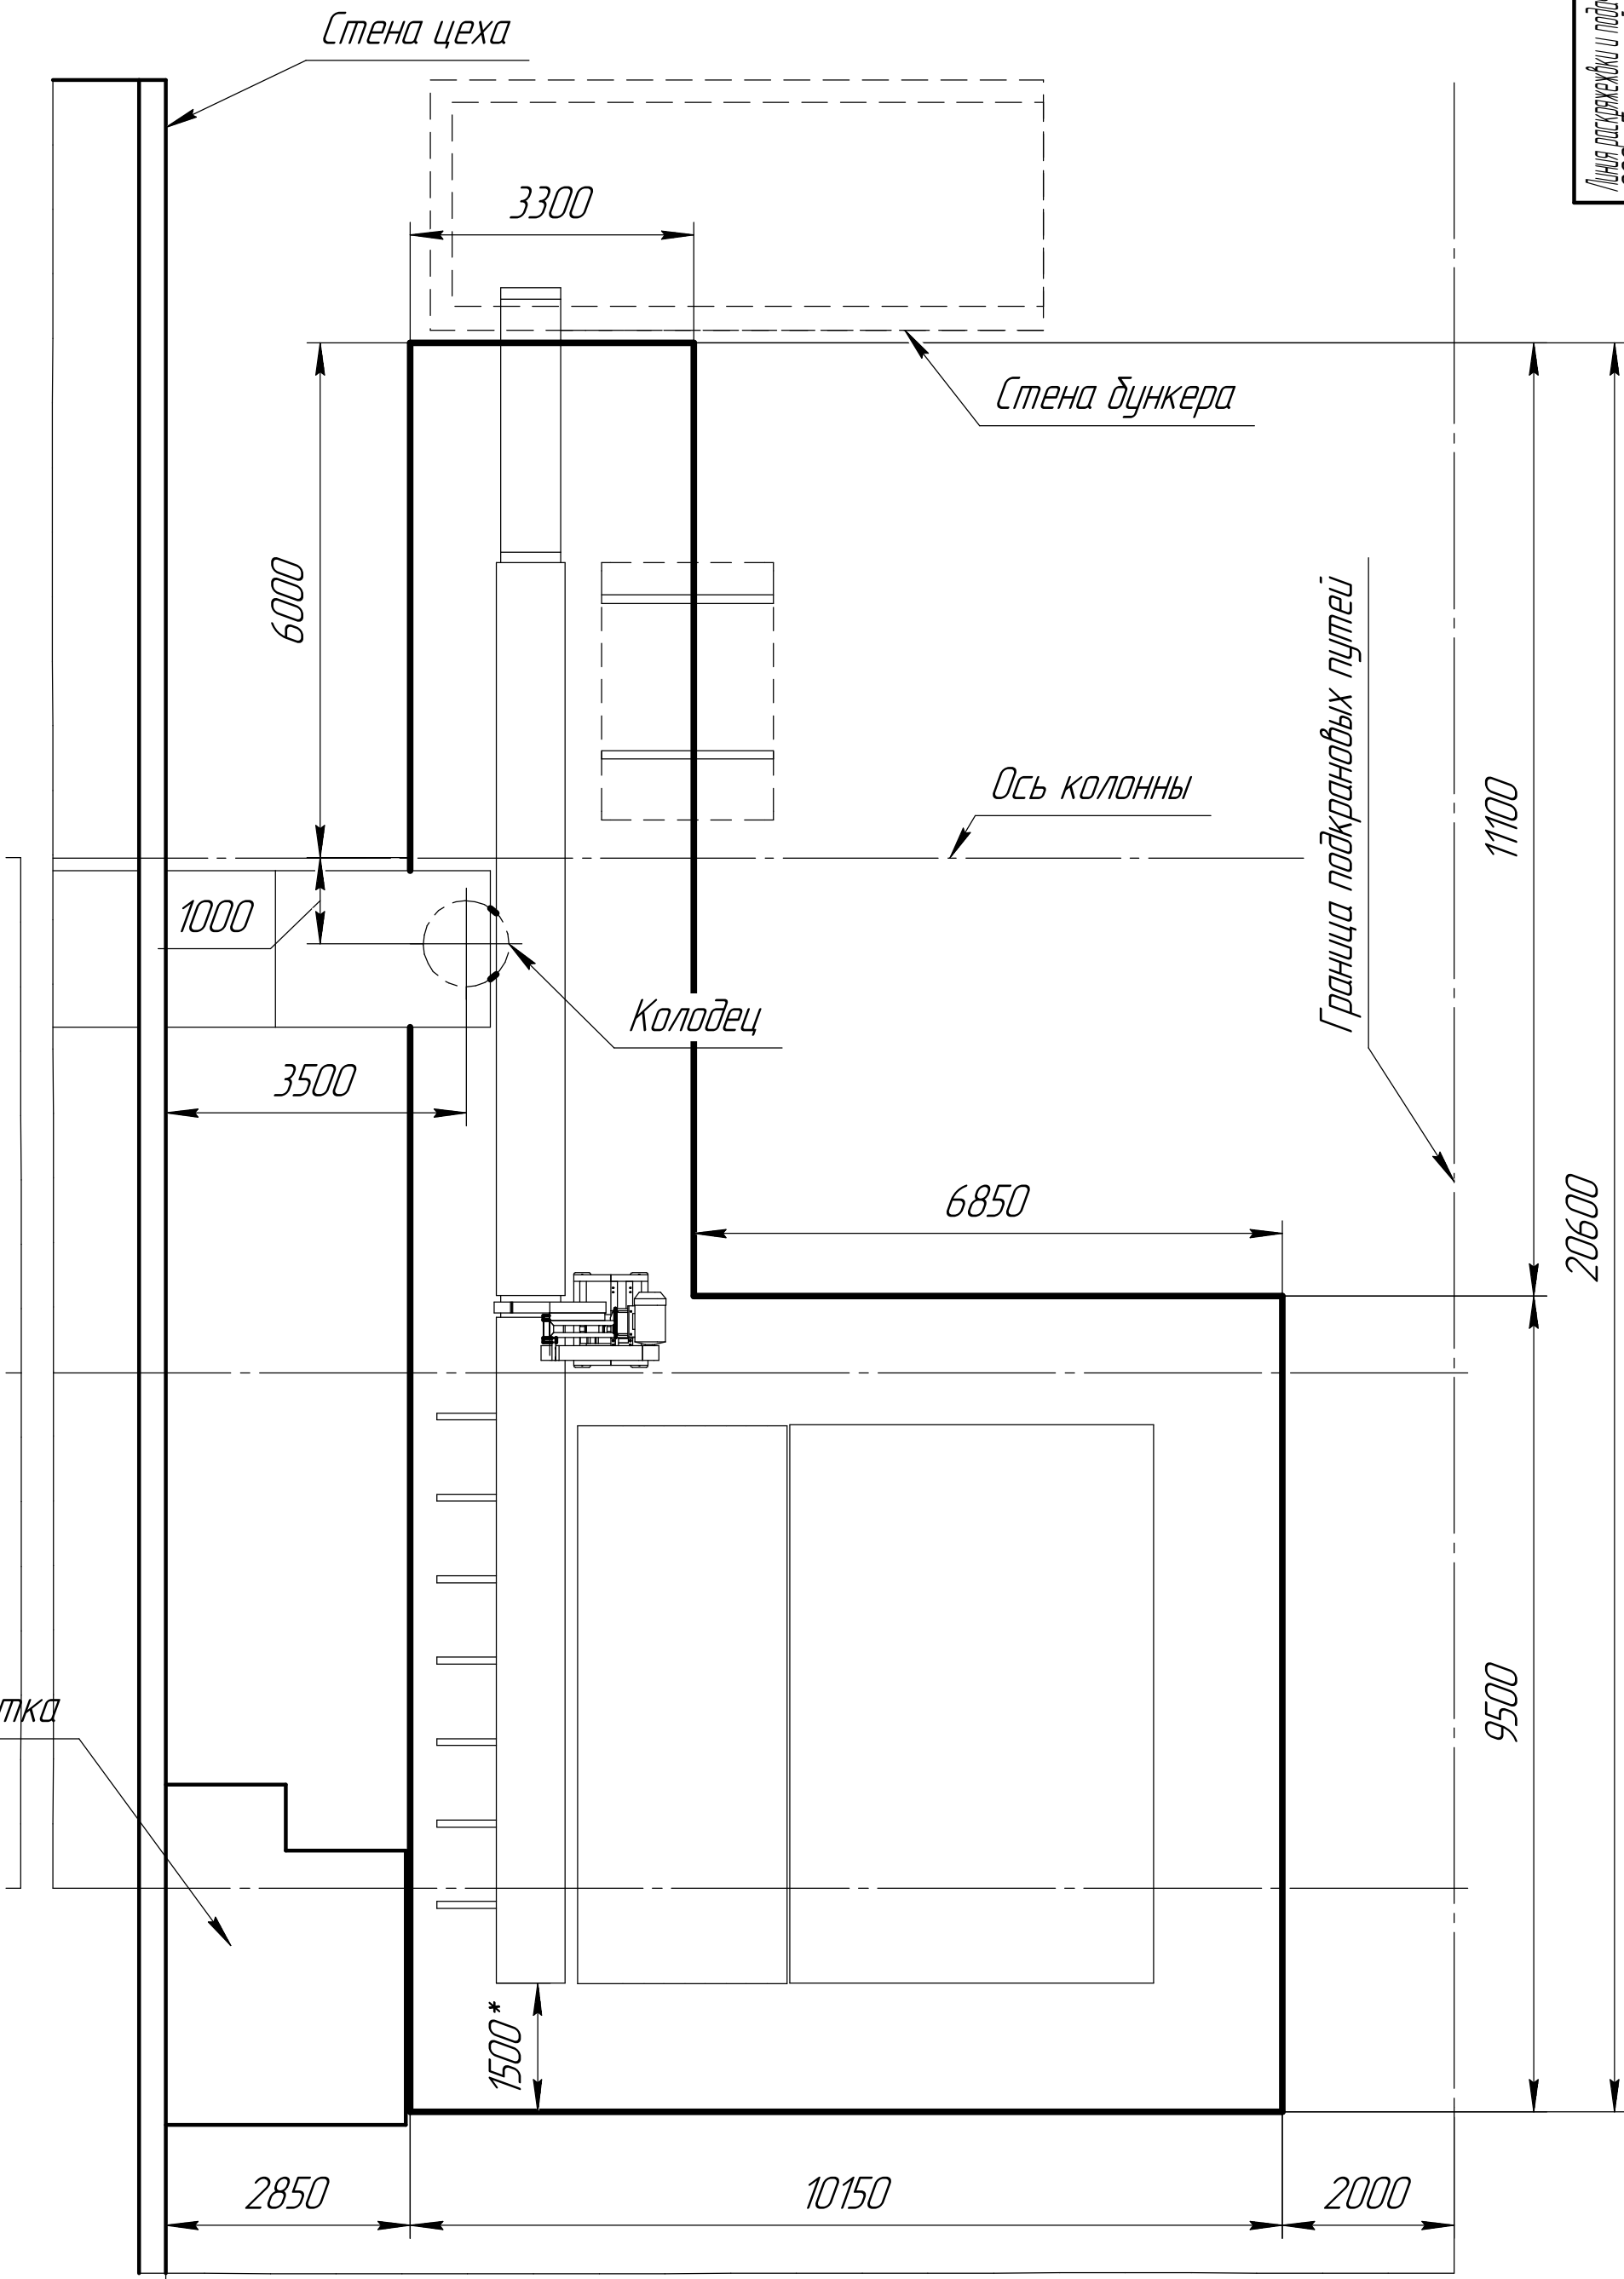

Инд. № подл.	Подп. и дата	Взам. инв. №	Инд. № дил.	Подп. и дата

Изм.	Лист	№ докум.	Подп.	Дата

Линия раскряжевки и подачи чураков на линию долуцивания
ООО «Галицкий фанерный комбинат»

Лист
5

Копировал

Формат А3

