



Обмерный план участка

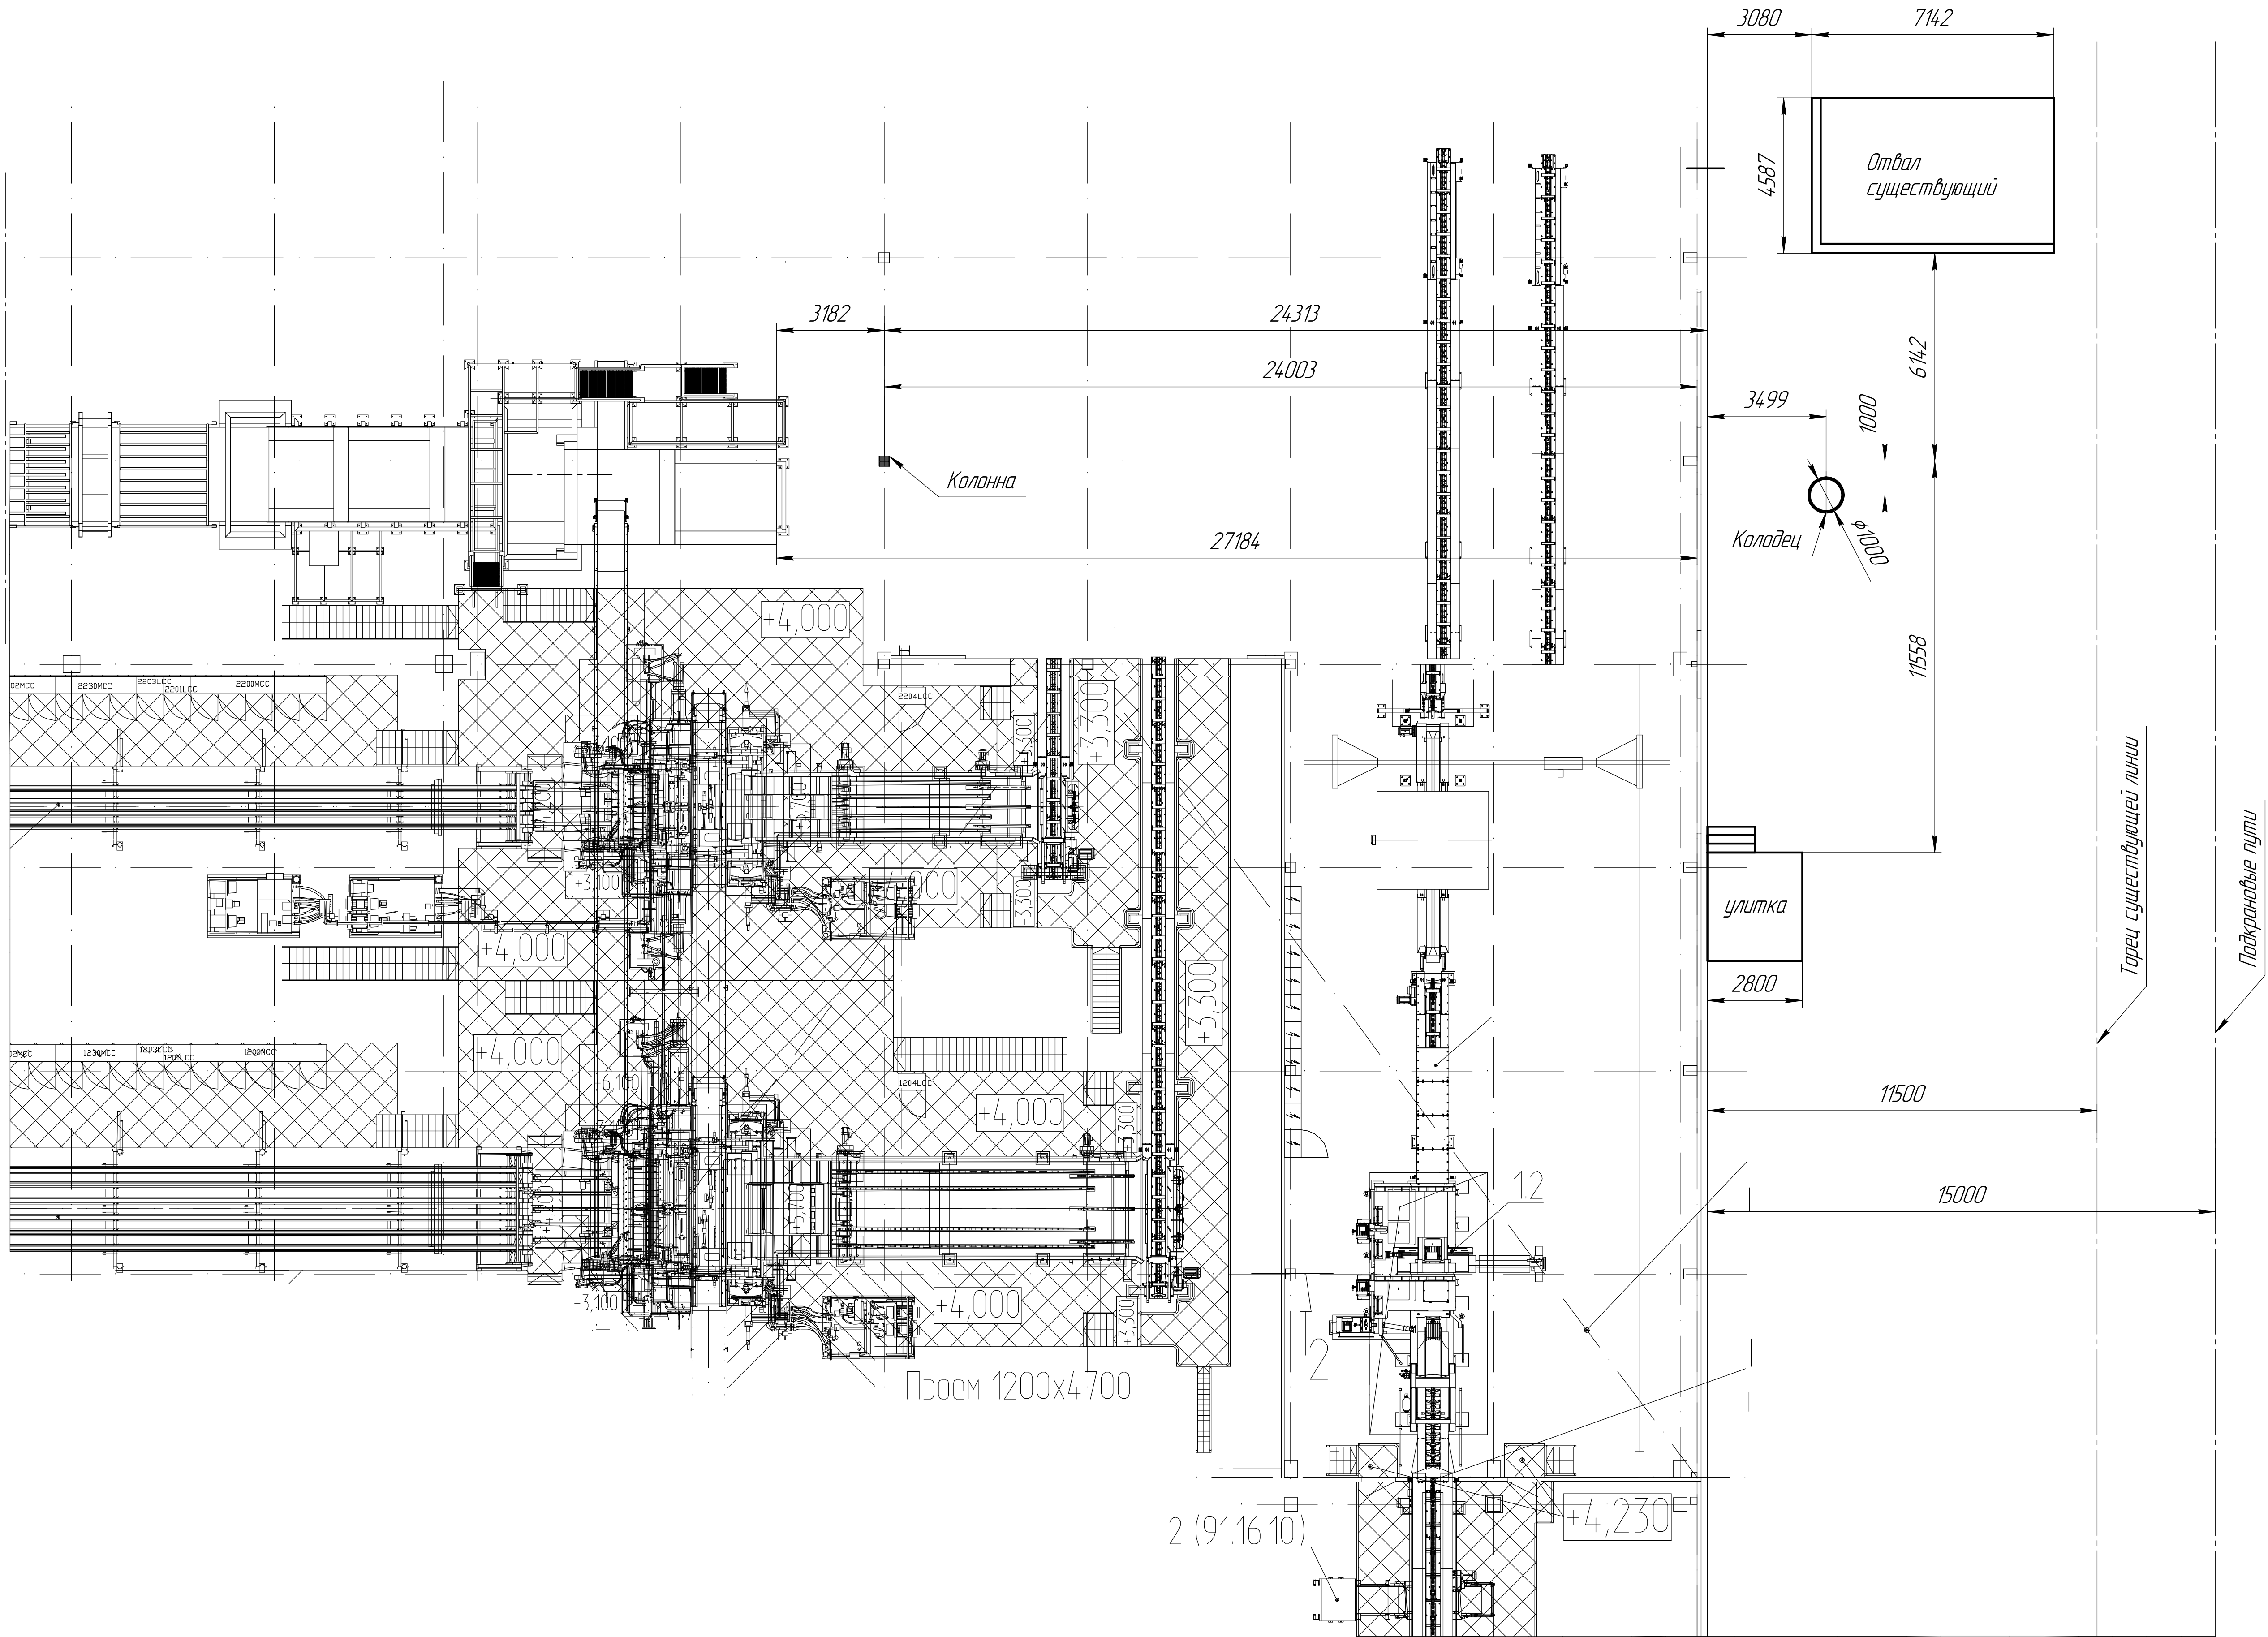


				Линия раскряжежки и подкрановые пути на линию дощичивания ООО «Галицкий фанерный комбинат»		
				План линии		
Изм.	Лист	№ док.	Подп.	Дат.	Лист	Масштаб
Разраб.					1	1:100
Проб.					1	1:100
Т.контр.					1	1:100
Н.контр.					1	1:100
Утв.					1	1:100
				ООО "ПО "ДИАКОМ"		
				Формат А1		

Схема расположения оборудования ПО "ДИАКОМ"

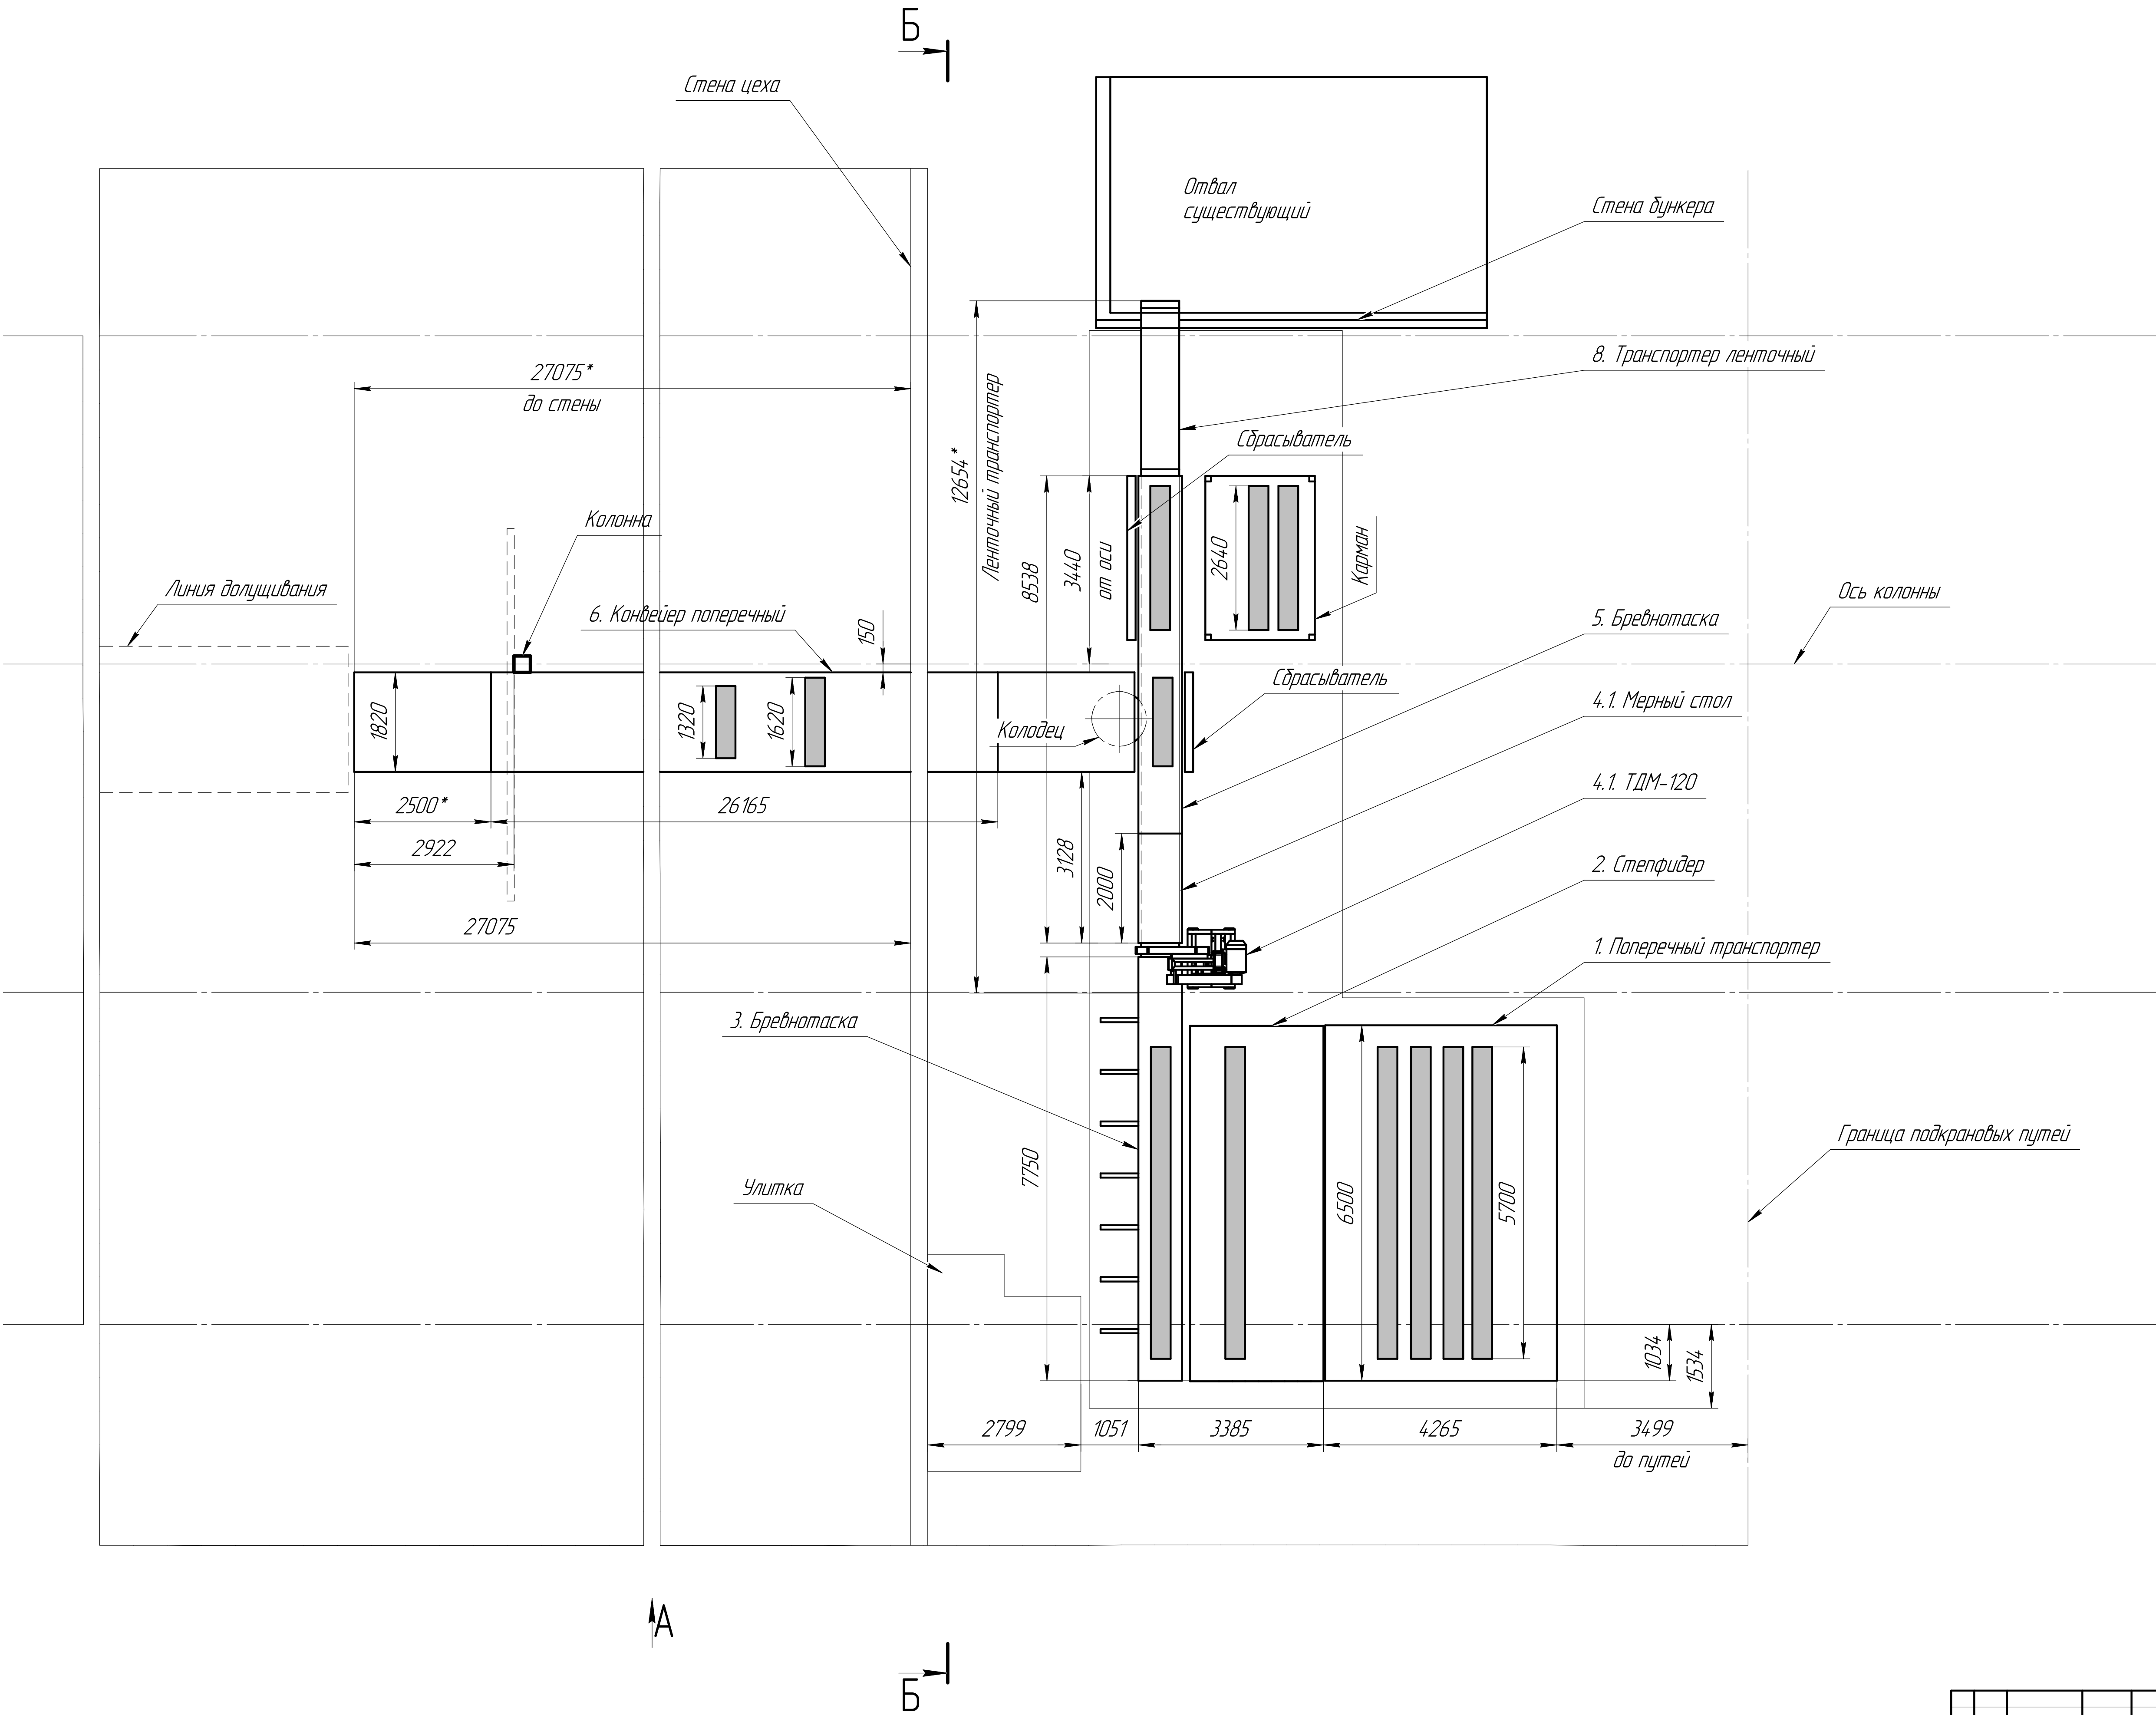


Б-Б^О
Высотные отметки оснований оборудования

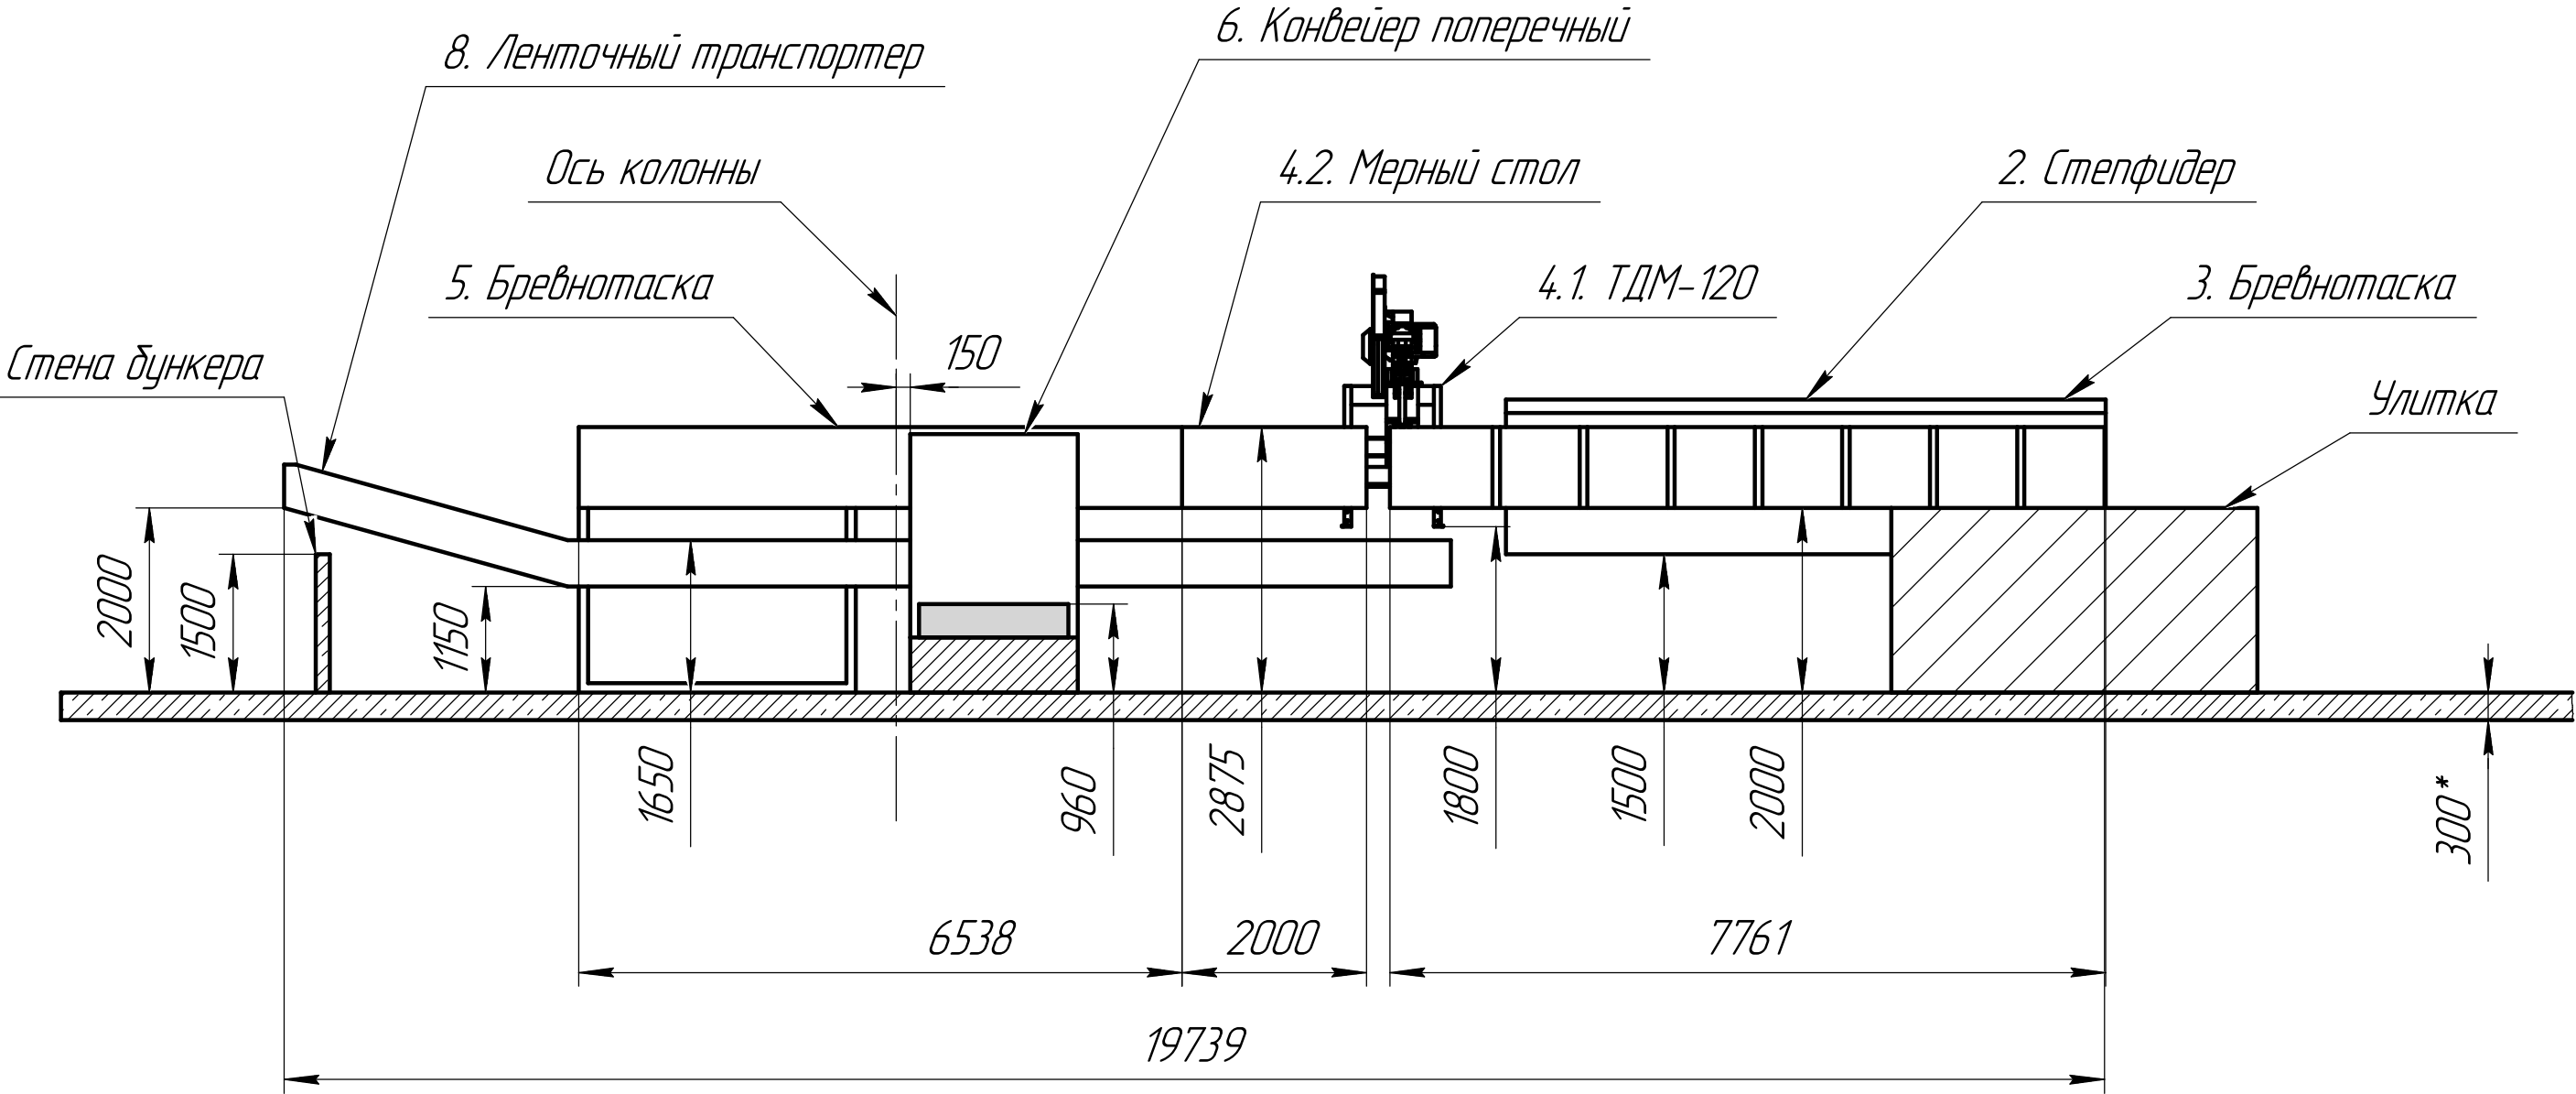

Изм. № подл.	Подп. и дата
Взам. инв. №	Инв. № докл.
Подп. и дата	Подп. и дата

А


Высотные отметки оснований оборудования

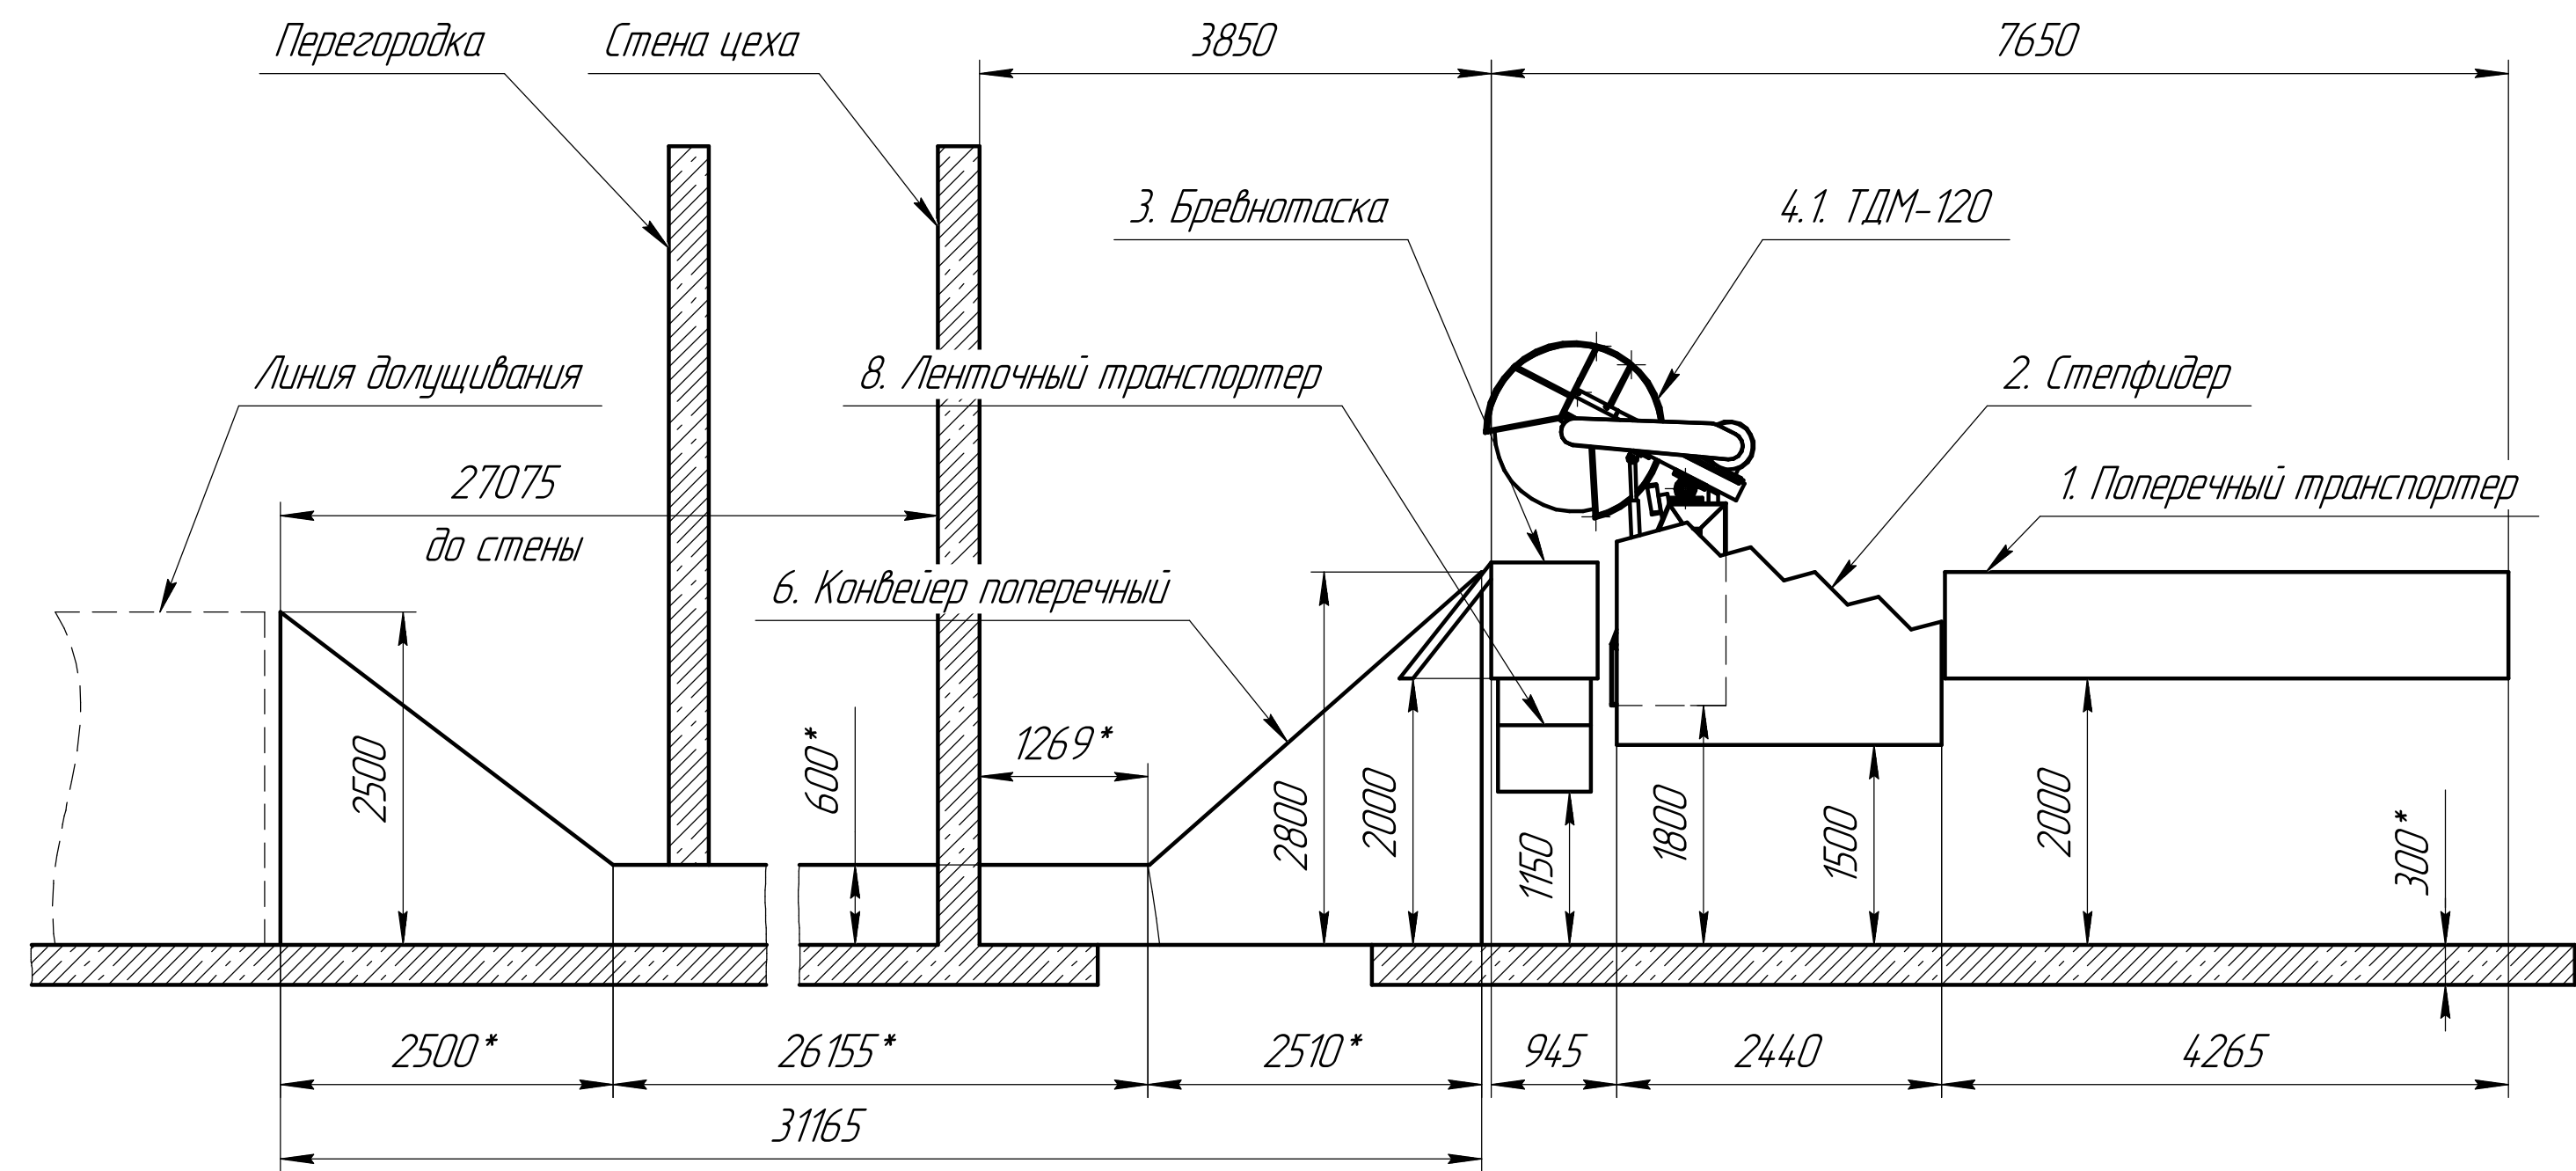

Изм.	Лист	№ докум.	Подп.	Дата
Изм.	Лист	№ докум.	Подп.	Дата
Изм.	Лист	№ докум.	Подп.	Дата
Изм.	Лист	№ докум.	Подп.	Дата
Изм.	Лист	№ докум.	Подп.	Дата

Габаритные размеры фундаментной плиты

Линия раскроежки и подачи чураков на линию долуцивания
ООО «Галицкий фанерный комбинат»

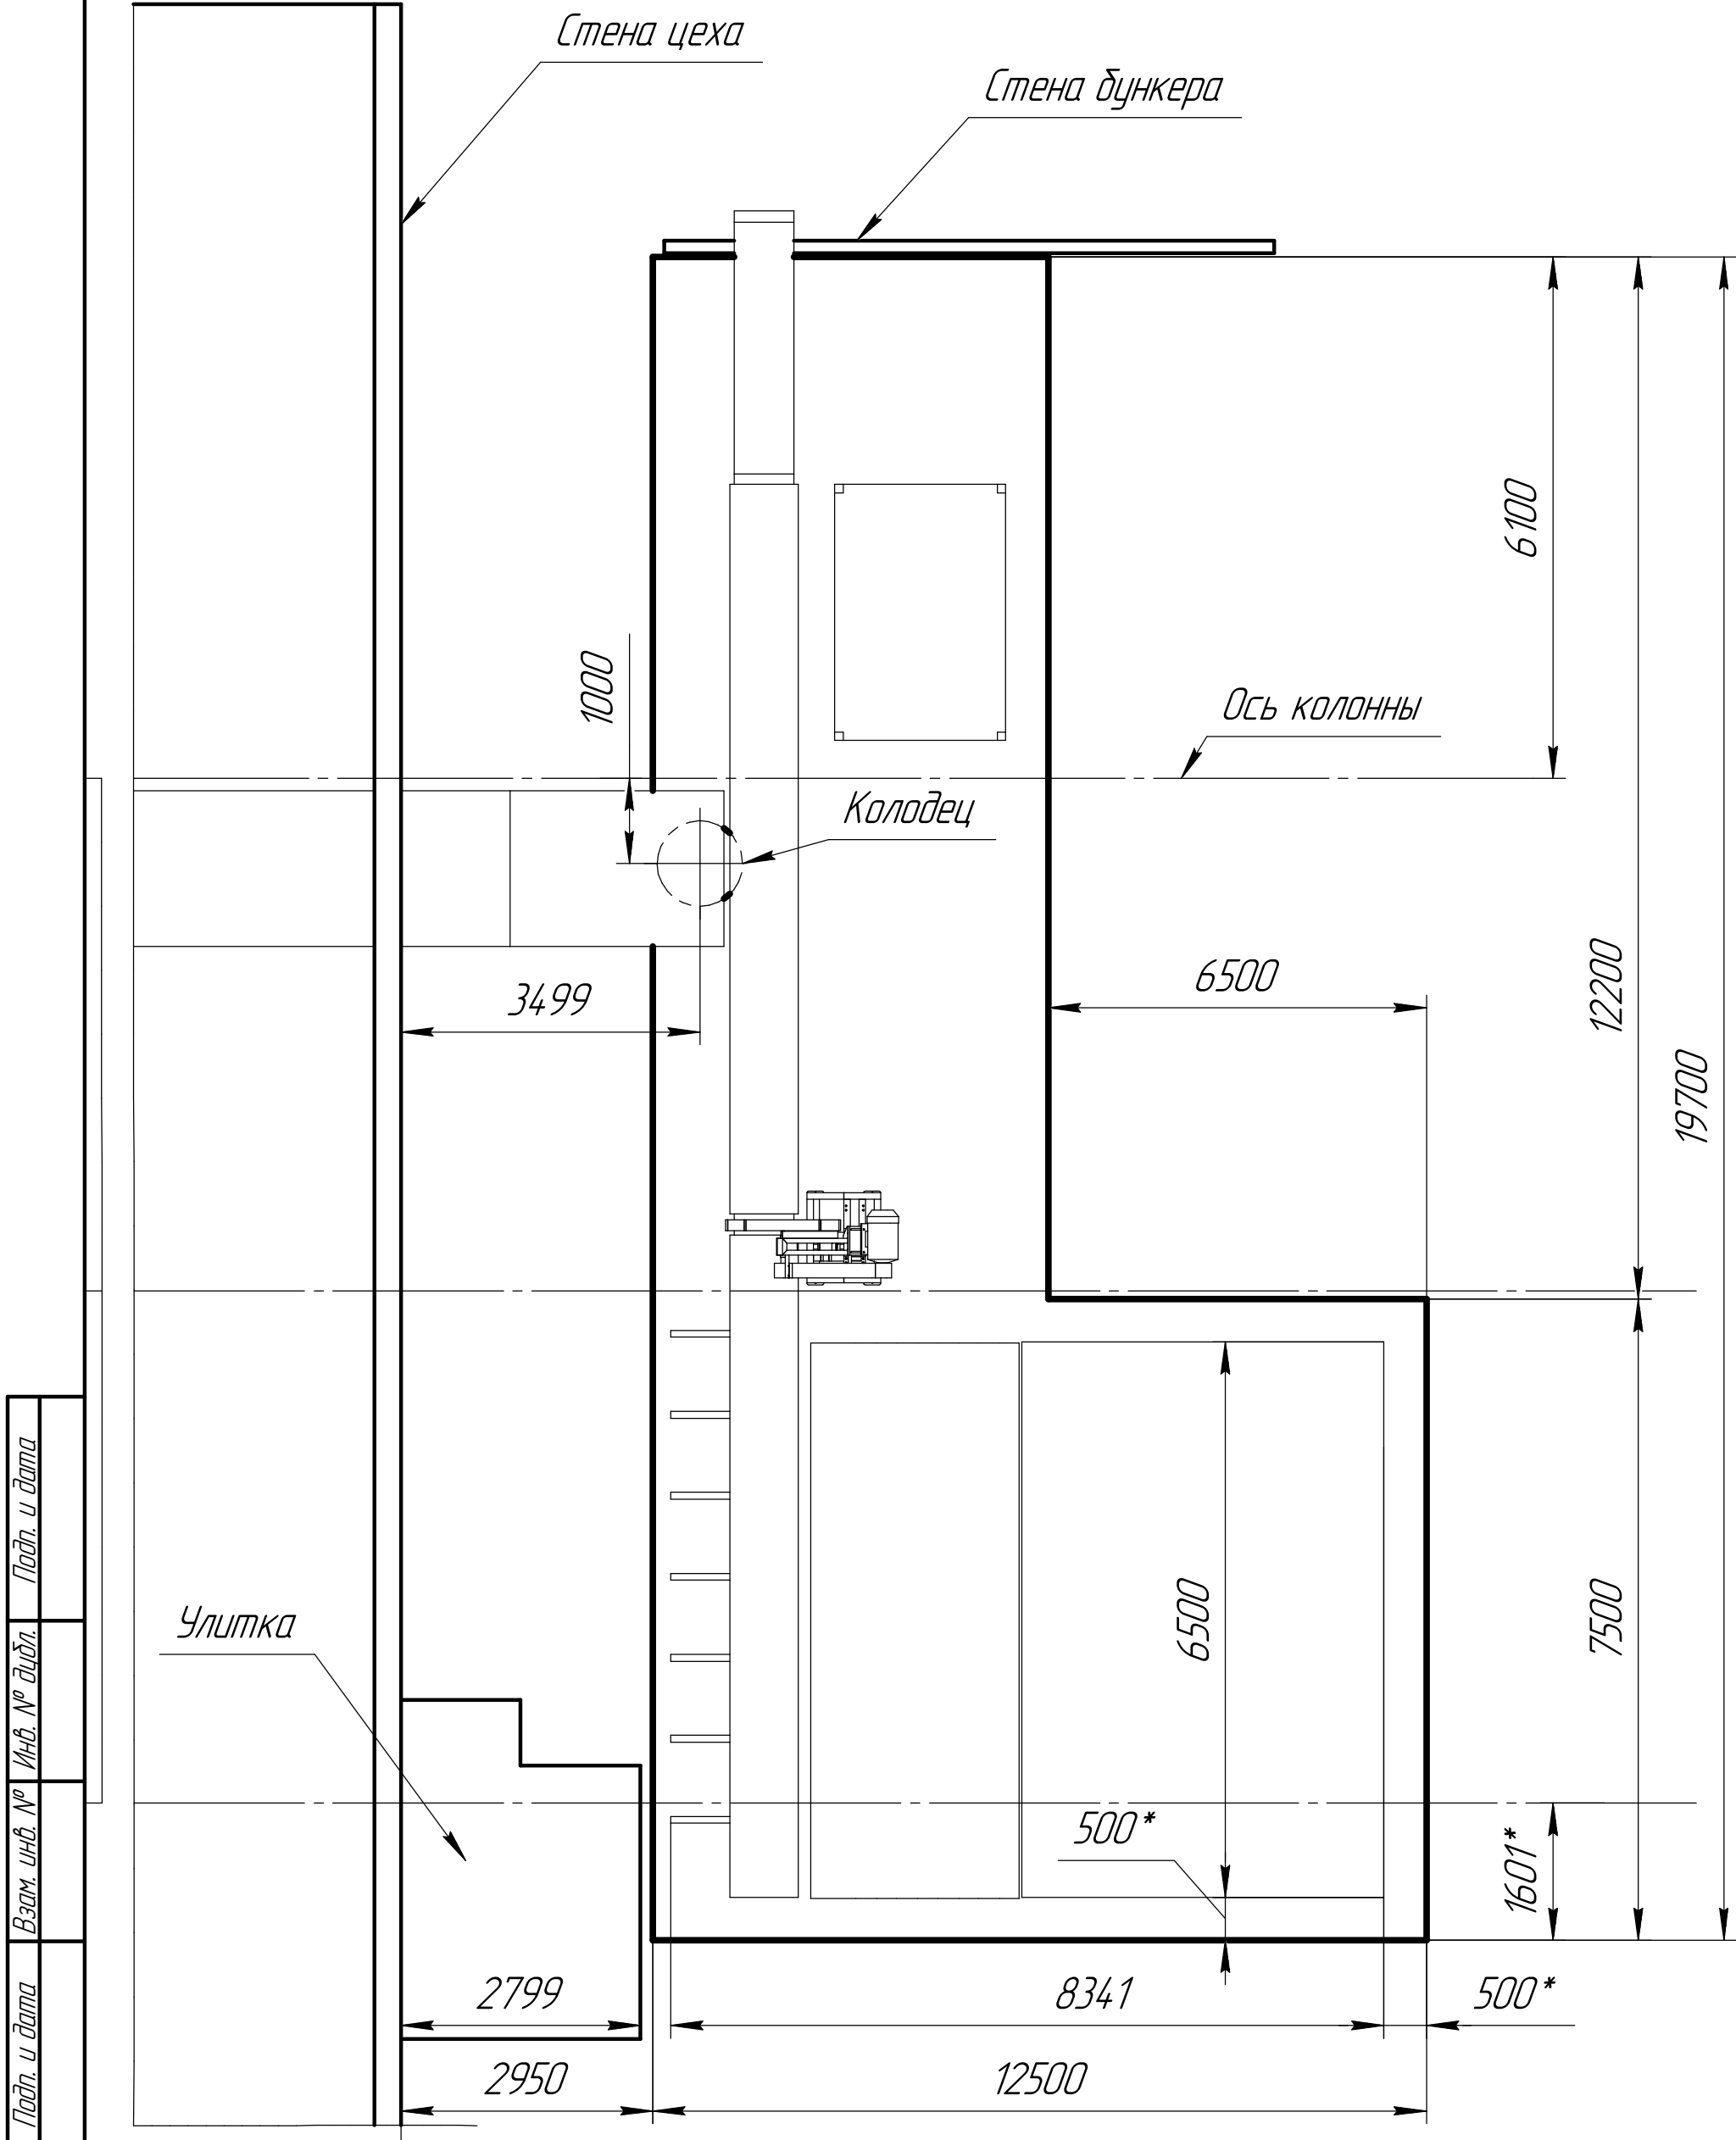

Инв. № подл.	Подп. и дата	Взам. инв. №	Инв. № докл.	Подп. и дата

Изм.	Лист	№ докум.	Подп.	Дата


Линия раскроежки и подачи чураков на линию долуцивания
ООО «Галицкий фанерный комбинат»

Лист
5

Копировал

Формат А3

Фундаментная плита

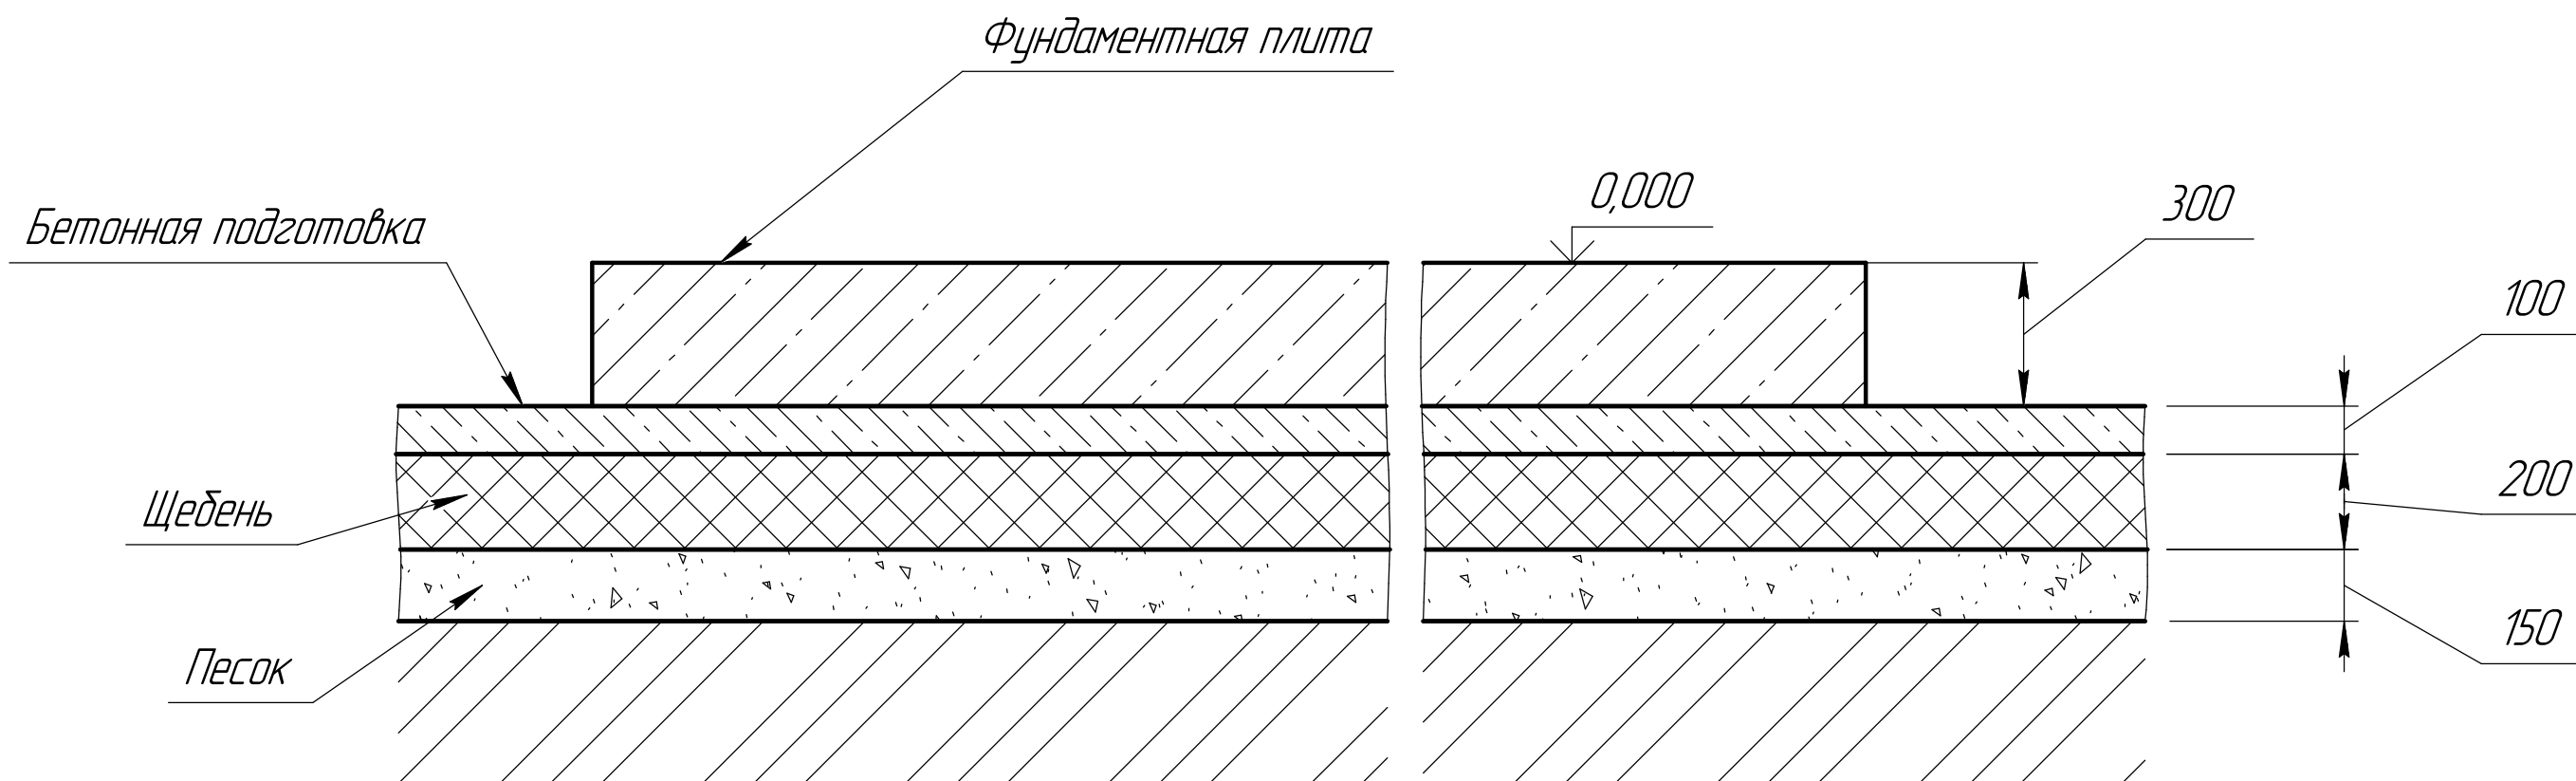

1. Принять рекомендуемую высоту бетонной армированной плиты 300 мм
2. Подготовить основание под плиту исходя из существующих грунтов (зависит от объема выемки грунта): на утрамбованное основание после выемки растительного и рыхлого слоя грунта уложить песок не менее 150мм, щебень не менее 200мм, Бетон В7,5 не менее 100мм.