


Инв. № подл.	Подп. и дата	Взам. инв. №	Инв. № дудл.	Подп. и дата	Спроб. №	Перв. примен.

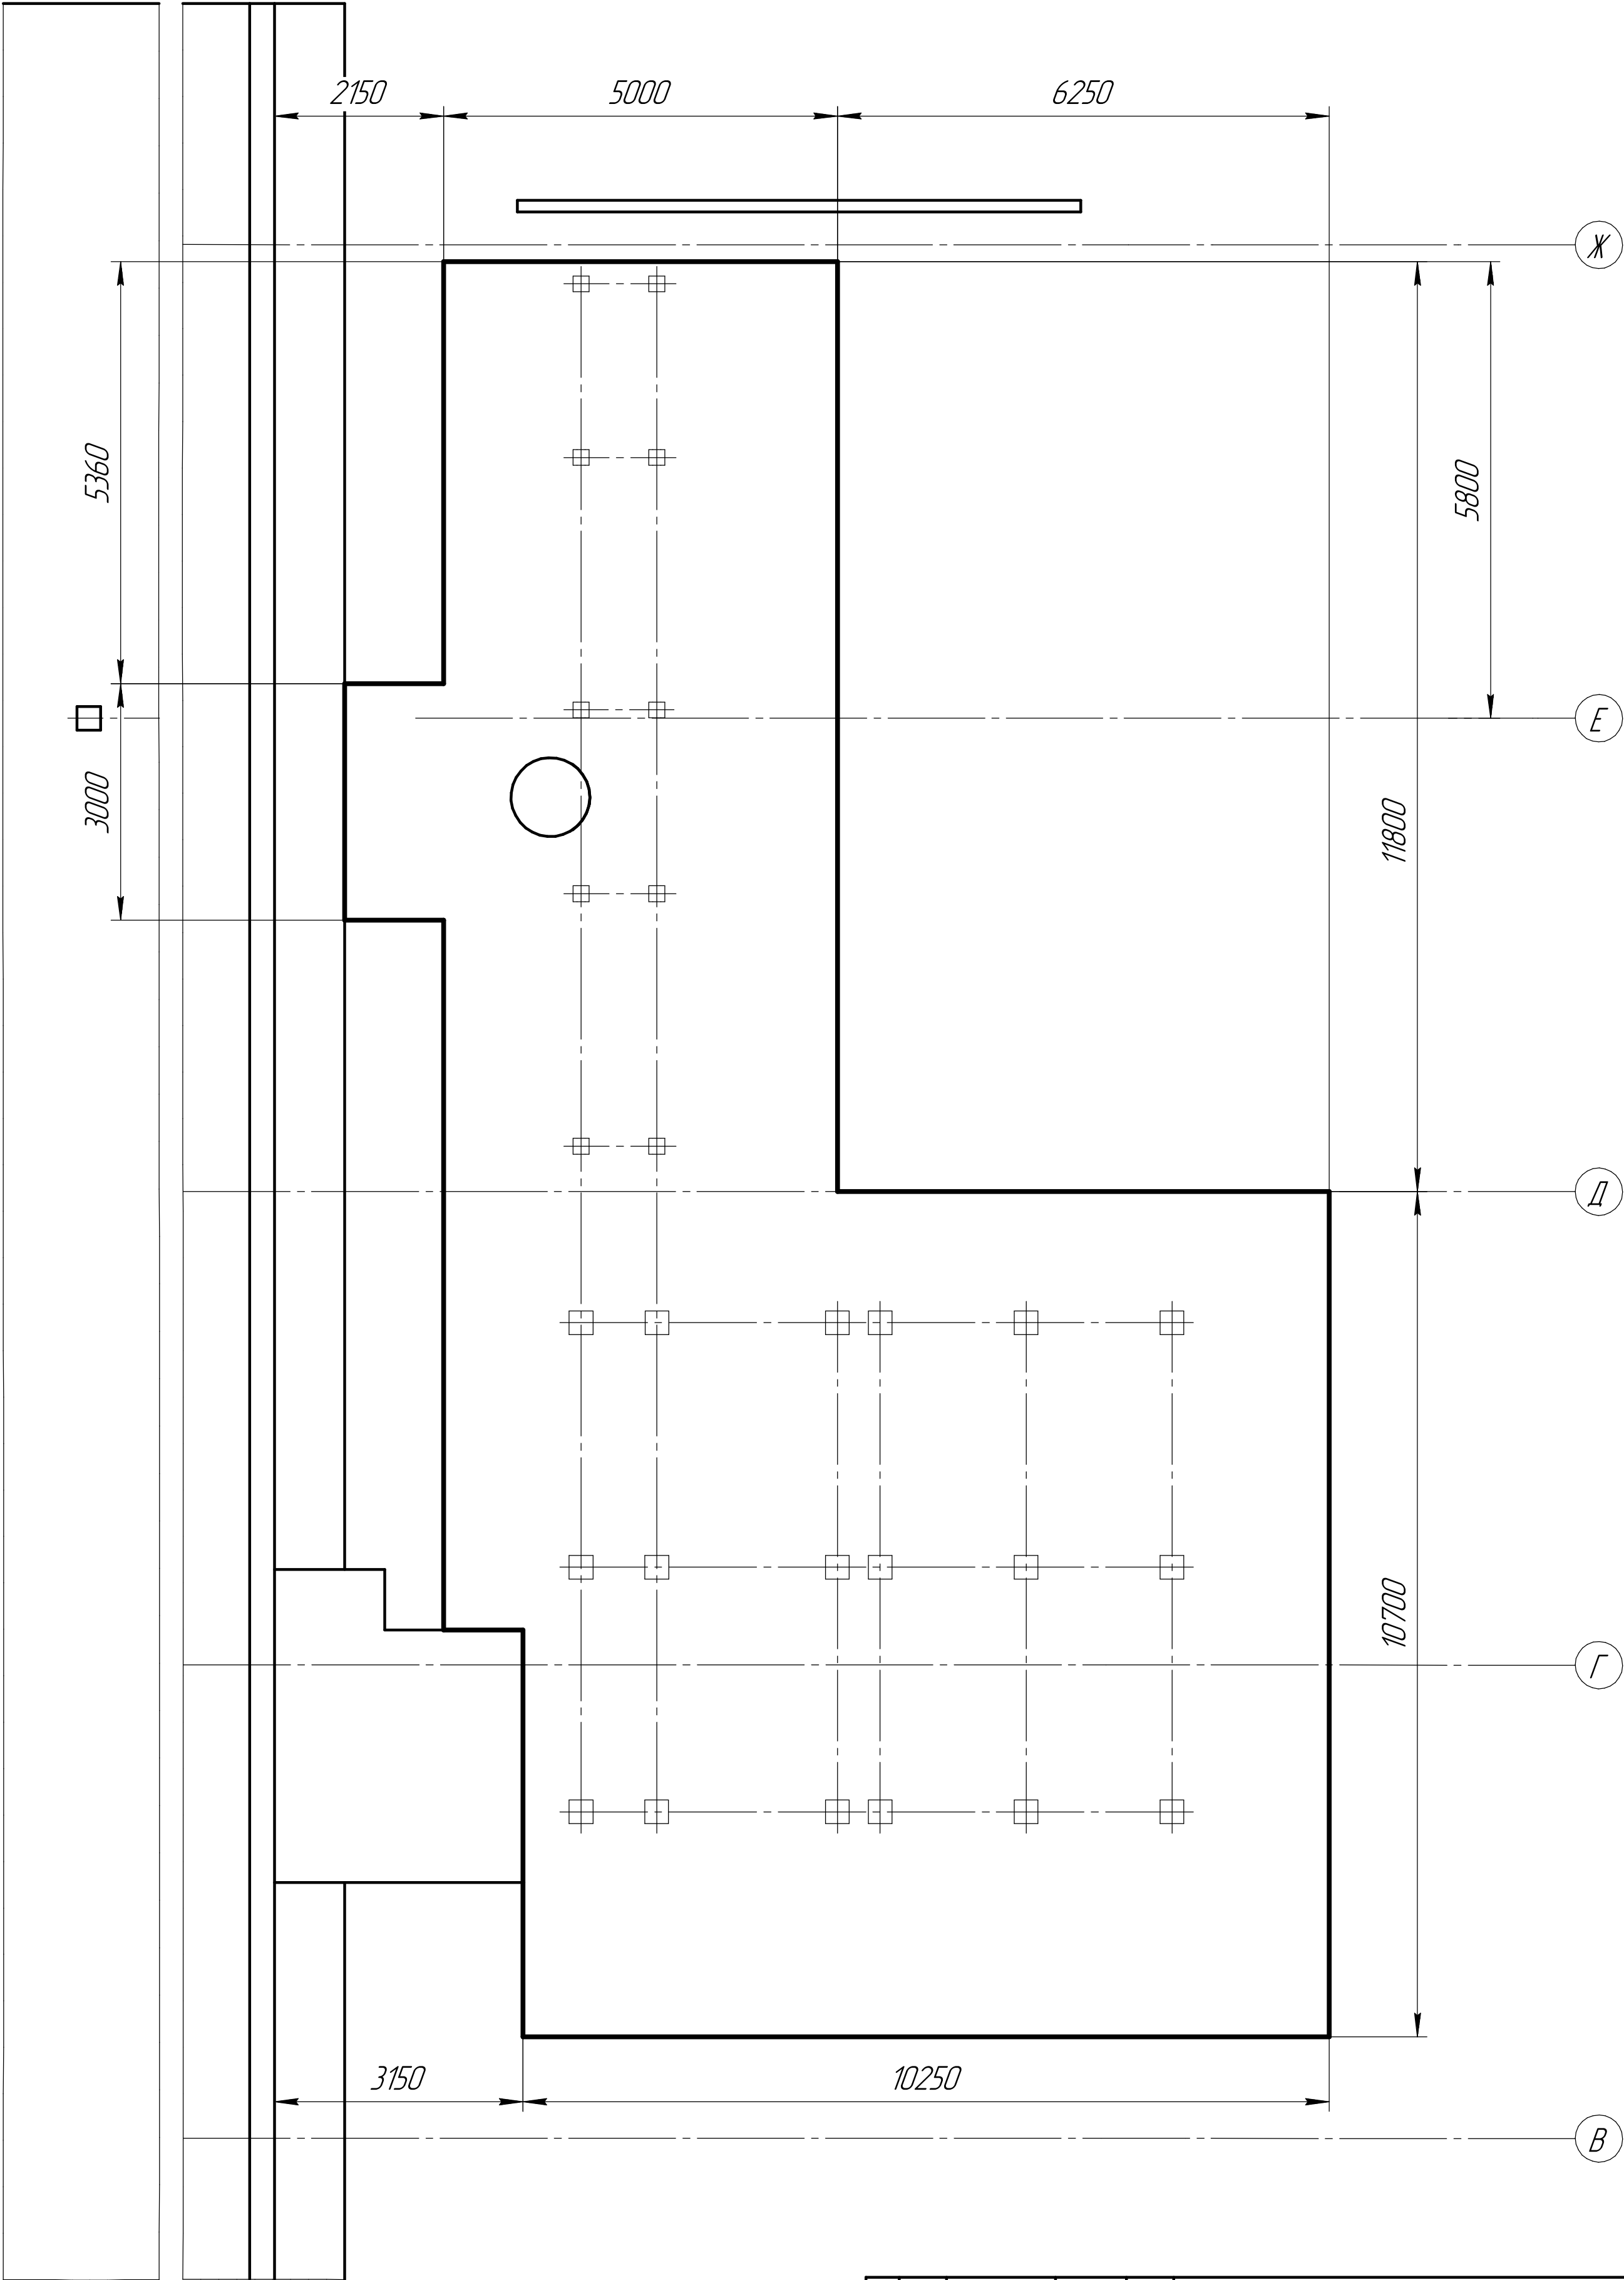


					ГФК				
Изм.	Лист	№ докум.	Подп.	Дата	План фундамента	Лит.	Масса	Масштаб	
Разраб.							1080544167	1:60	
Проб.						Лист	1	Листов	
Т.контр.								2	
Н.контр.						ПО "ДИАКОМ"			
Утв.									

ГФК

План закладных деталей

ГФК

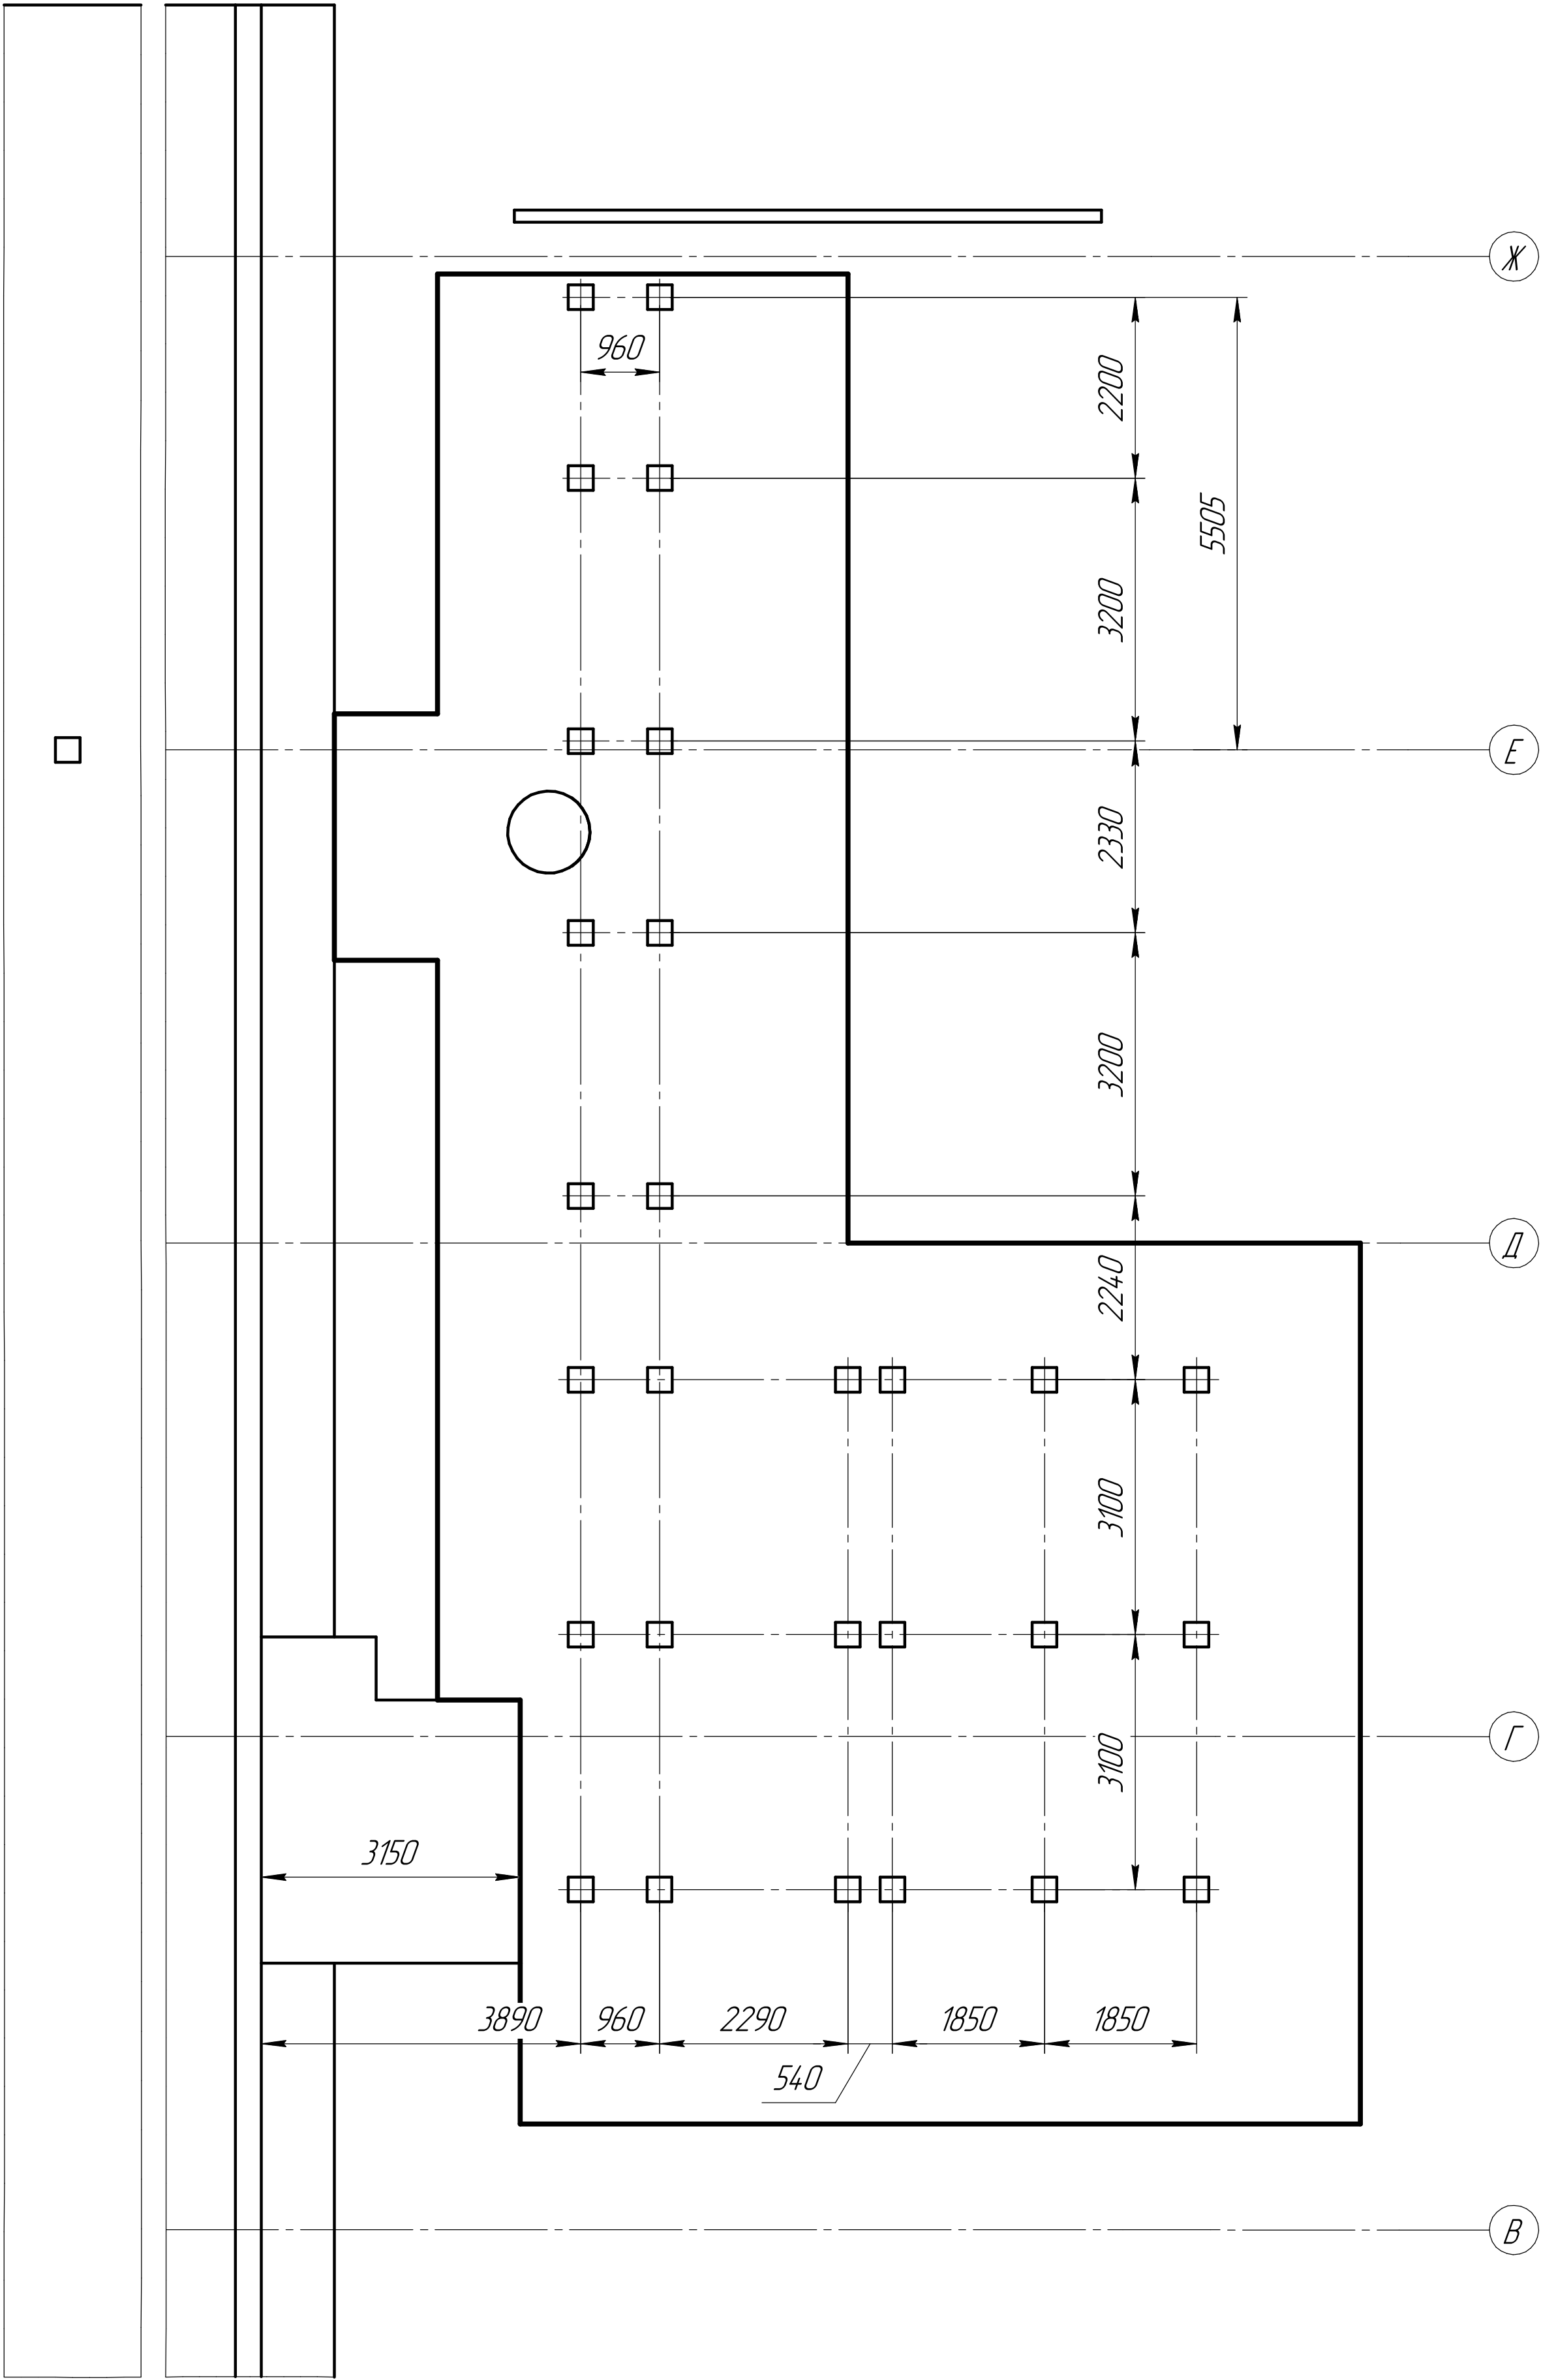

1. Размер закладной подобрать под опору колонны 250х250 мм.

Инд. № подл.	Подп. и дата	Взам. инд. №	Инд. № ауд.	Подп. и дата

Изм.	Лист	№ докум.	Подп.	Дата

ГФК

Лист
2

Копировал

Формат А2